AIRCRAFT PARKING / DOCKING CHART - ICAO

APRON ELEV
105 ft

TWR	126.2
GND	121.95

DAEGU/Daegu INTL

ELEVATIONS IN FEET
DIMENSION IN METERS
BEARINGS ARE MAGNETIC

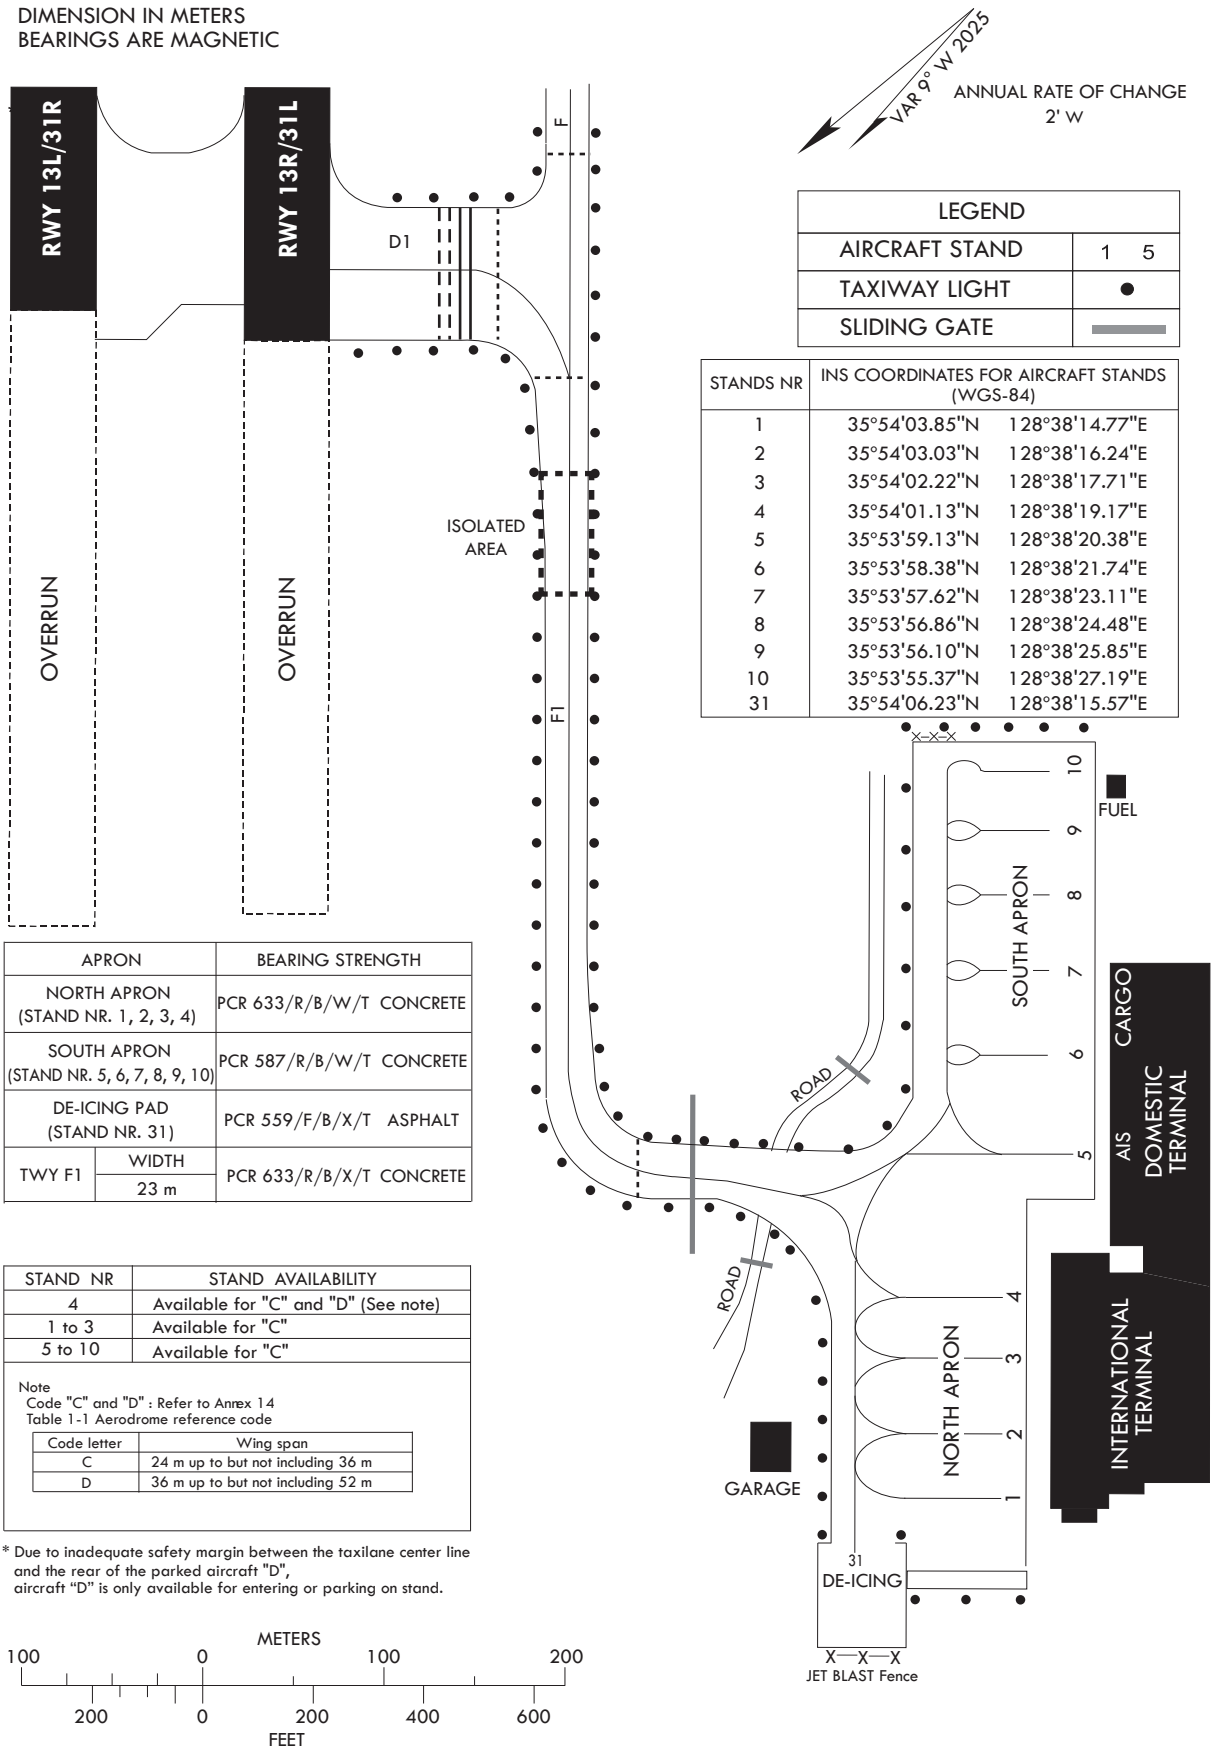

LEGEND	
AIRCRAFT STAND	1 5
TAXIWAY LIGHT	●
SLIDING GATE	▬

STANDS NR	INS COORDINATES FOR AIRCRAFT STANDS (WGS-84)	
1	35°54'03.85"N	128°38'14.77"E
2	35°54'03.03"N	128°38'16.24"E
3	35°54'02.22"N	128°38'17.71"E
4	35°54'01.13"N	128°38'19.17"E
5	35°53'59.13"N	128°38'20.38"E
6	35°53'58.38"N	128°38'21.74"E
7	35°53'57.62"N	128°38'23.11"E
8	35°53'56.86"N	128°38'24.48"E
9	35°53'56.10"N	128°38'25.85"E
10	35°53'55.37"N	128°38'27.19"E
31	35°54'06.23"N	128°38'15.57"E

APRON		BEARING STRENGTH
NORTH APRON (STAND NR. 1, 2, 3, 4)		PCR 633/R/B/W/T CONCRETE
SOUTH APRON (STAND NR. 5, 6, 7, 8, 9, 10)		PCR 587/R/B/W/T CONCRETE
DE-ICING PAD (STAND NR. 31)		PCR 559/F/B/X/T ASPHALT
TWY F1	WIDTH 23 m	PCR 633/R/B/X/T CONCRETE

STAND NR	STAND AVAILABILITY
4	Available for "C" and "D" (See note)
1 to 3	Available for "C"
5 to 10	Available for "C"

Note
Code "C" and "D" : Refer to Annex 14
Table 1-1 Aerodrome reference code

Code letter	Wing span
C	24 m up to but not including 36 m
D	36 m up to but not including 52 m

* Due to inadequate safety margin between the taxilane center line and the rear of the parked aircraft "D", aircraft "D" is only available for entering or parking on stand.

Change : Information of surface for TWY.

INTENTIONALLY

LEFT

BLANK