


AIRCRAFT PARKING
DOCKING CHART - ICAO

APRON ELEV
8 ft

TWR	118.1	118.450
	233.3	236.6
GND	121.9	275.8
APRON	121.65	317.450

BUSAN/Gimhae INTL

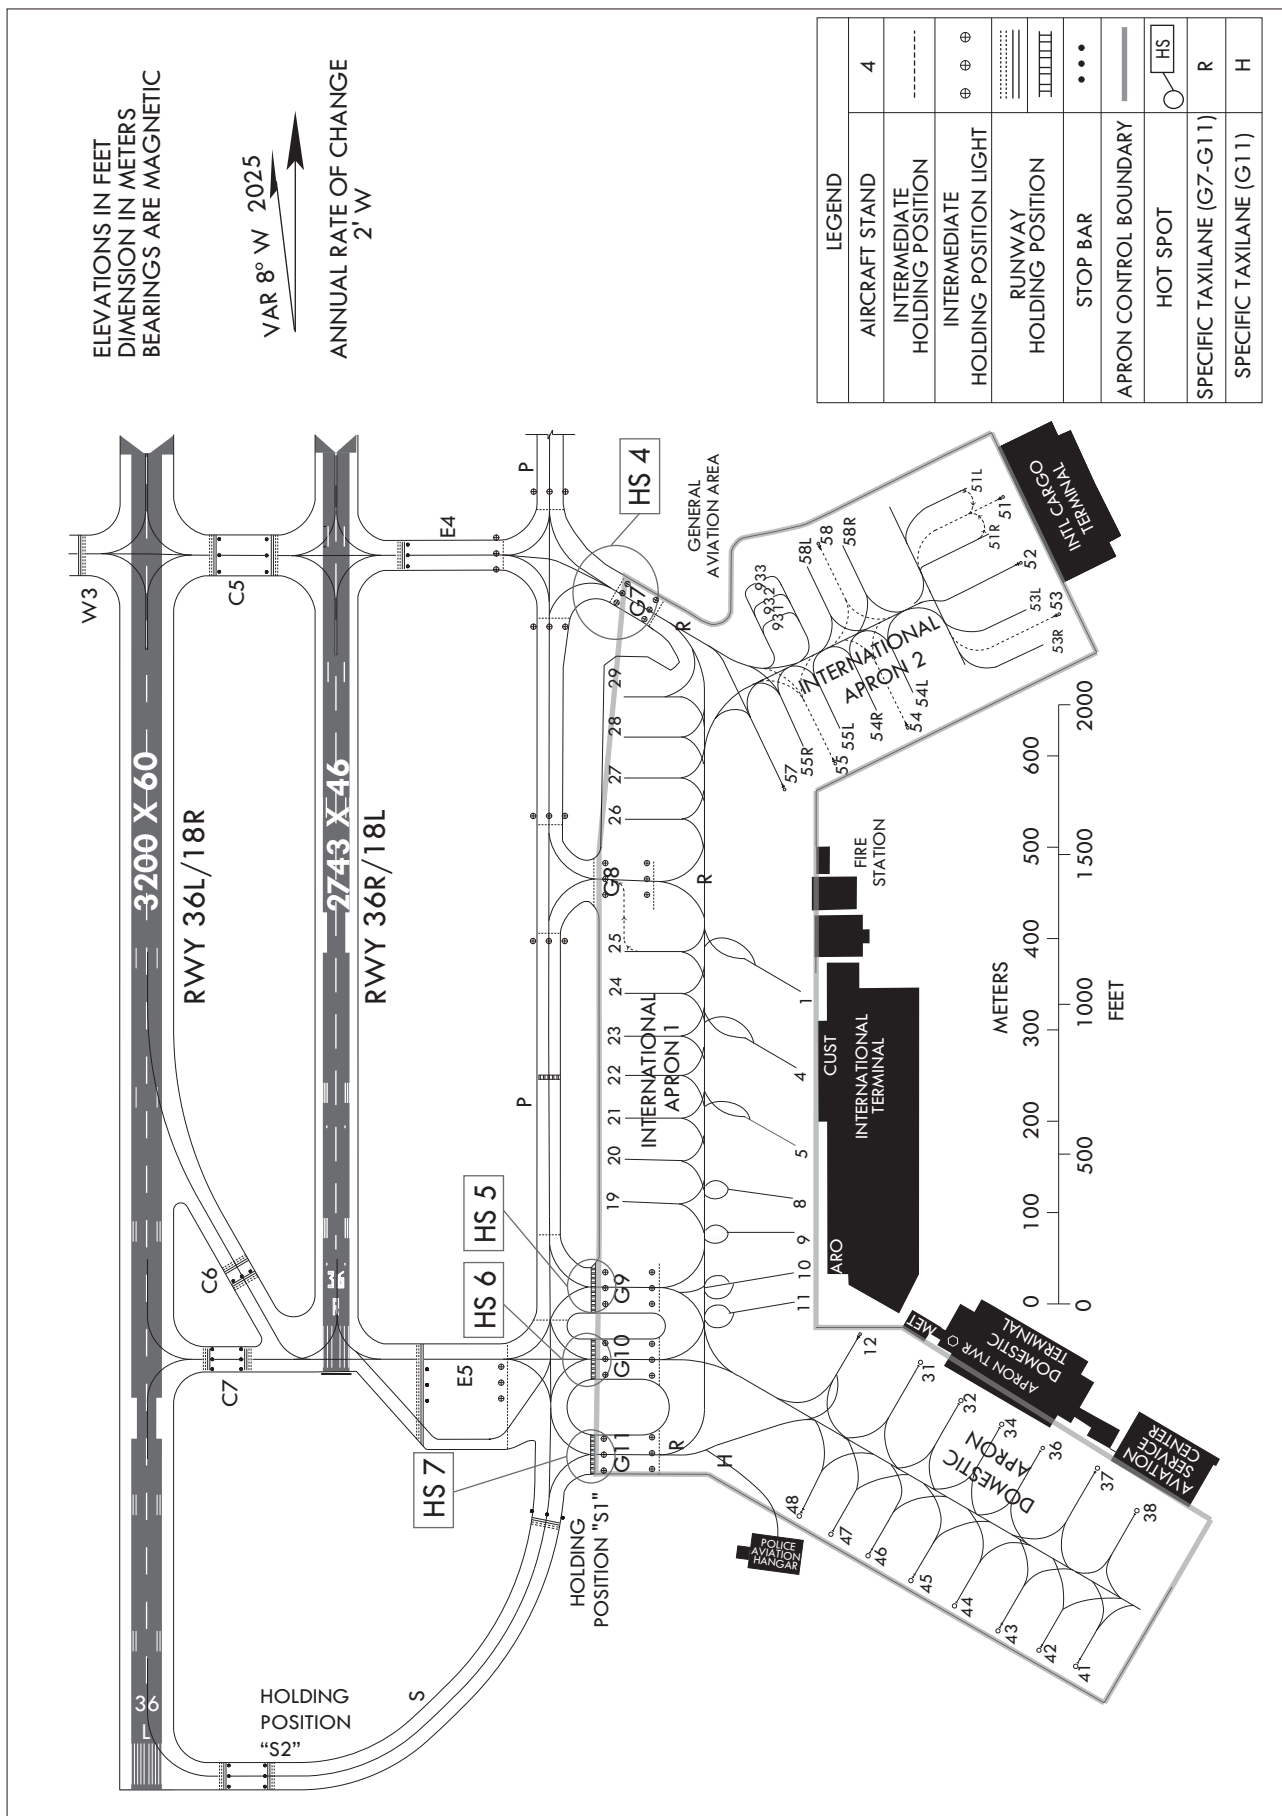

Change : Information of name of office(AIS → ARO).

INS COORDINATES FOR AIRCRAFT STANDS(WGS-84)				TAXIWAY INFORMATION			AIRCRAFT STANDS	
				TAXIWAY	WIDTH(m)	STRENGTH(PCR)		
1	35°10'25.69"N	128°56'44.55"E	58	35°10'41.49"N	30	1 178 R/C/W/T	1, 53	B747-400, A340-600
4	35°10'22.90"N	128°56'44.89"E	58L	35°10'40.71"N	30	1 178 R/C/W/T		
5	35°10'20.12"N	128°56'45.24"E	58R	35°10'41.49"N		662 F/B/X/T	4, 12, 51, 54, 55	B747-400
8	35°10'18.30"N	128°56'45.10"E	931	35°10'38.86"N	30	1 006 R/B/W/T	5, 37	A350-900
9	35°10'16.92"N	128°56'45.43"E	932	35°10'39.47"N		621 F/A/X/T		
10	35°10'15.69"N	128°56'45.62"E	933	35°10'40.07"N	30	1 006 R/B/W/T	31	B777-200
11	35°10'14.25"N	128°56'46.11"E				1 006 R/B/W/T		
12	35°10'13.59"N	128°56'48.90"E			30	621 F/A/X/T	58	A350-900, B787-10
19	35°10'17.50"N	128°56'37.69"E						
20	35°10'18.98"N	128°56'37.50"E			23	1 178 R/C/W/T		
21	35°10'20.46"N	128°56'37.31"E			45	1 178 R/C/W/T	45	B767-300ERW
22	35°10'21.95"N	128°56'37.12"E			78	1 178 R/C/W/T	43	B767-300
23	35°10'23.43"N	128°56'36.93"E				N/A		
24	35°10'24.92"N	128°56'36.74"E			(Military maintenance taxiway)		8, 9, 10, 11, 19, 20, 21, 22, 23, 24, 25, 26, 27, 28, 29, 32, 34, 36, 38, 41, 42, 44, 46, 47, 48, 51L, 51R, 52, 53L, 53R, 54L, 54R, 55L, 55R, 57, 58L, 58R	B737 MAX 9, A321 NEO
25	35°10'26.40"N	128°56'36.54"E				496 F/B/X/T	※ ISOLATED STAND : E1	
26	35°10'31.10"N	128°56'36.39"E			44	1 178 R/C/W/T		
27	35°10'32.55"N	128°56'36.20"E				496 F/B/X/T		
28	35°10'34.00"N	128°56'36.01"E			44	1 178 R/C/W/T		
29	35°10'35.46"N	128°56'35.82"E						
31	35°10'12.79"N	128°56'51.56"E						
32	35°10'11.61"N	128°56'53.51"E						
34	35°10'10.92"N	128°56'55.39"E						
36	35°10'10.21"N	128°56'57.21"E				662 F/B/X/T		
37	35°10'09.69"N	128°56'59.68"E				621 F/A/X/T		
38	35°10'08.34"N	128°57'01.60"E						
41	35°10'02.85"N	128°56'59.81"E						
42	35°10'03.30"N	128°56'58.18"E						
43	35°10'03.83"N	128°56'56.31"E						
44	35°10'04.56"N	128°56'54.32"E						
45	35°10'05.29"N	128°56'52.33"E						
46	35°10'06.01"N	128°56'50.37"E						
47	35°10'06.62"N	128°56'48.62"E						
48	35°10'07.47"N	128°56'47.16"E						
51	35°10'43.74"N	128°56'50.99"E						
51L	35°10'44.10"N	128°56'49.58"E						
51R	35°10'42.55"N	128°56'50.77"E						
52	35°10'41.51"N	128°56'52.08"E						
53	35°10'39.81"N	128°56'54.00"E						
53L	35°10'40.03"N	128°56'52.71"E						
53R	35°10'38.83"N	128°56'53.63"E						
54	35°10'35.46"N	128°56'48.11"E						
54L	35°10'36.65"N	128°56'48.25"E						
54R	35°10'35.87"N	128°56'46.74"E						
55	35°10'33.92"N	128°56'45.12"E						
55L	35°10'35.10"N	128°56'45.24"E						
55R	35°10'34.33"N	128°56'43.74"E						
57	35°10'32.82"N	128°56'43.03"E						

INS COORDINATES FOR AIRCRAFT STANDS(WGS-84)			
58	35°10'41.49"N	128°56'43.51"E	
58L	35°10'40.71"N	128°56'43.08"E	
58R	35°10'41.49"N	128°56'44.56"E	
931	35°10'38.86"N	128°56'42.15"E	
932	35°10'39.47"N	128°56'41.69"E	
933	35°10'40.07"N	128°56'41.22"E	

TAXIWAY INFORMATION			AIRCRAFT STANDS	
TAXIWAY	WIDTH(m)	STRENGTH(PCR)		
P	30	1 178 R/C/W/T	1, 53	B747-400, A340-600
E1, E2, E3, E4, E5	30	1 178 R/C/W/T		
		662 F/B/X/T	4, 12, 51, 54, 55	B747-400
S	30	1 006 R/B/W/T	5, 37	A350-900
		621 F/A/X/T		
C5	30	1 006 R/B/W/T	31	B777-200
		1 006 R/B/W/T		
C1, C2, C3, C4, C6, C7	30	621 F/A/X/T	58	A350-900, B787-10
G7	23	1 178 R/C/W/T		
G8	45	1 178 R/C/W/T	45	B767-300ERW
G9	78	1 178 R/C/W/T	43	B767-300
W2		N/A		
W3		(Military maintenance taxiway)		
		496 F/B/X/T		
G10	44	1 178 R/C/W/T		
		496 F/B/X/T		
G11	44	1 178 R/C/W/T		
W1, G1, G2, G3, G4, G5, G6		N/A (Military use taxiway)		
R	-	662 F/B/X/T		
H	-	621 F/A/X/T		

APRON INFORMATION	
APRON	STRENGTH(PCR)
INTERNATIONAL 1	662 F/B/X/T
DOMESTIC	621 F/A/X/T
INTERNATIONAL 2	1 178 R/C/W/T

REMARKS	
AS-365, EC-155, AW-139, S-76C, KA-32	

* Dimensions means overall length x width.

DEICING PAD			
INS COORDINATES FOR AIRCRAFT STANDS			
	WGS-84		ELEV(AMSL)
G8	35°10'28.65"N	128°56'35.67"E	8 ft
G9	35°10'14.68"N	128°56'37.42"E	8 ft
26	35°10'31.10"N	128°56'36.39"E	-
27	35°10'32.55"N	128°56'36.20"E	-