


AIRCRAFT PARKING/
DOCKING CHART - ICAO

APRON ELEV	
Central Apron	16 m
The Other	13 m

TWR	118.1
GND	121.9
APN	130.875

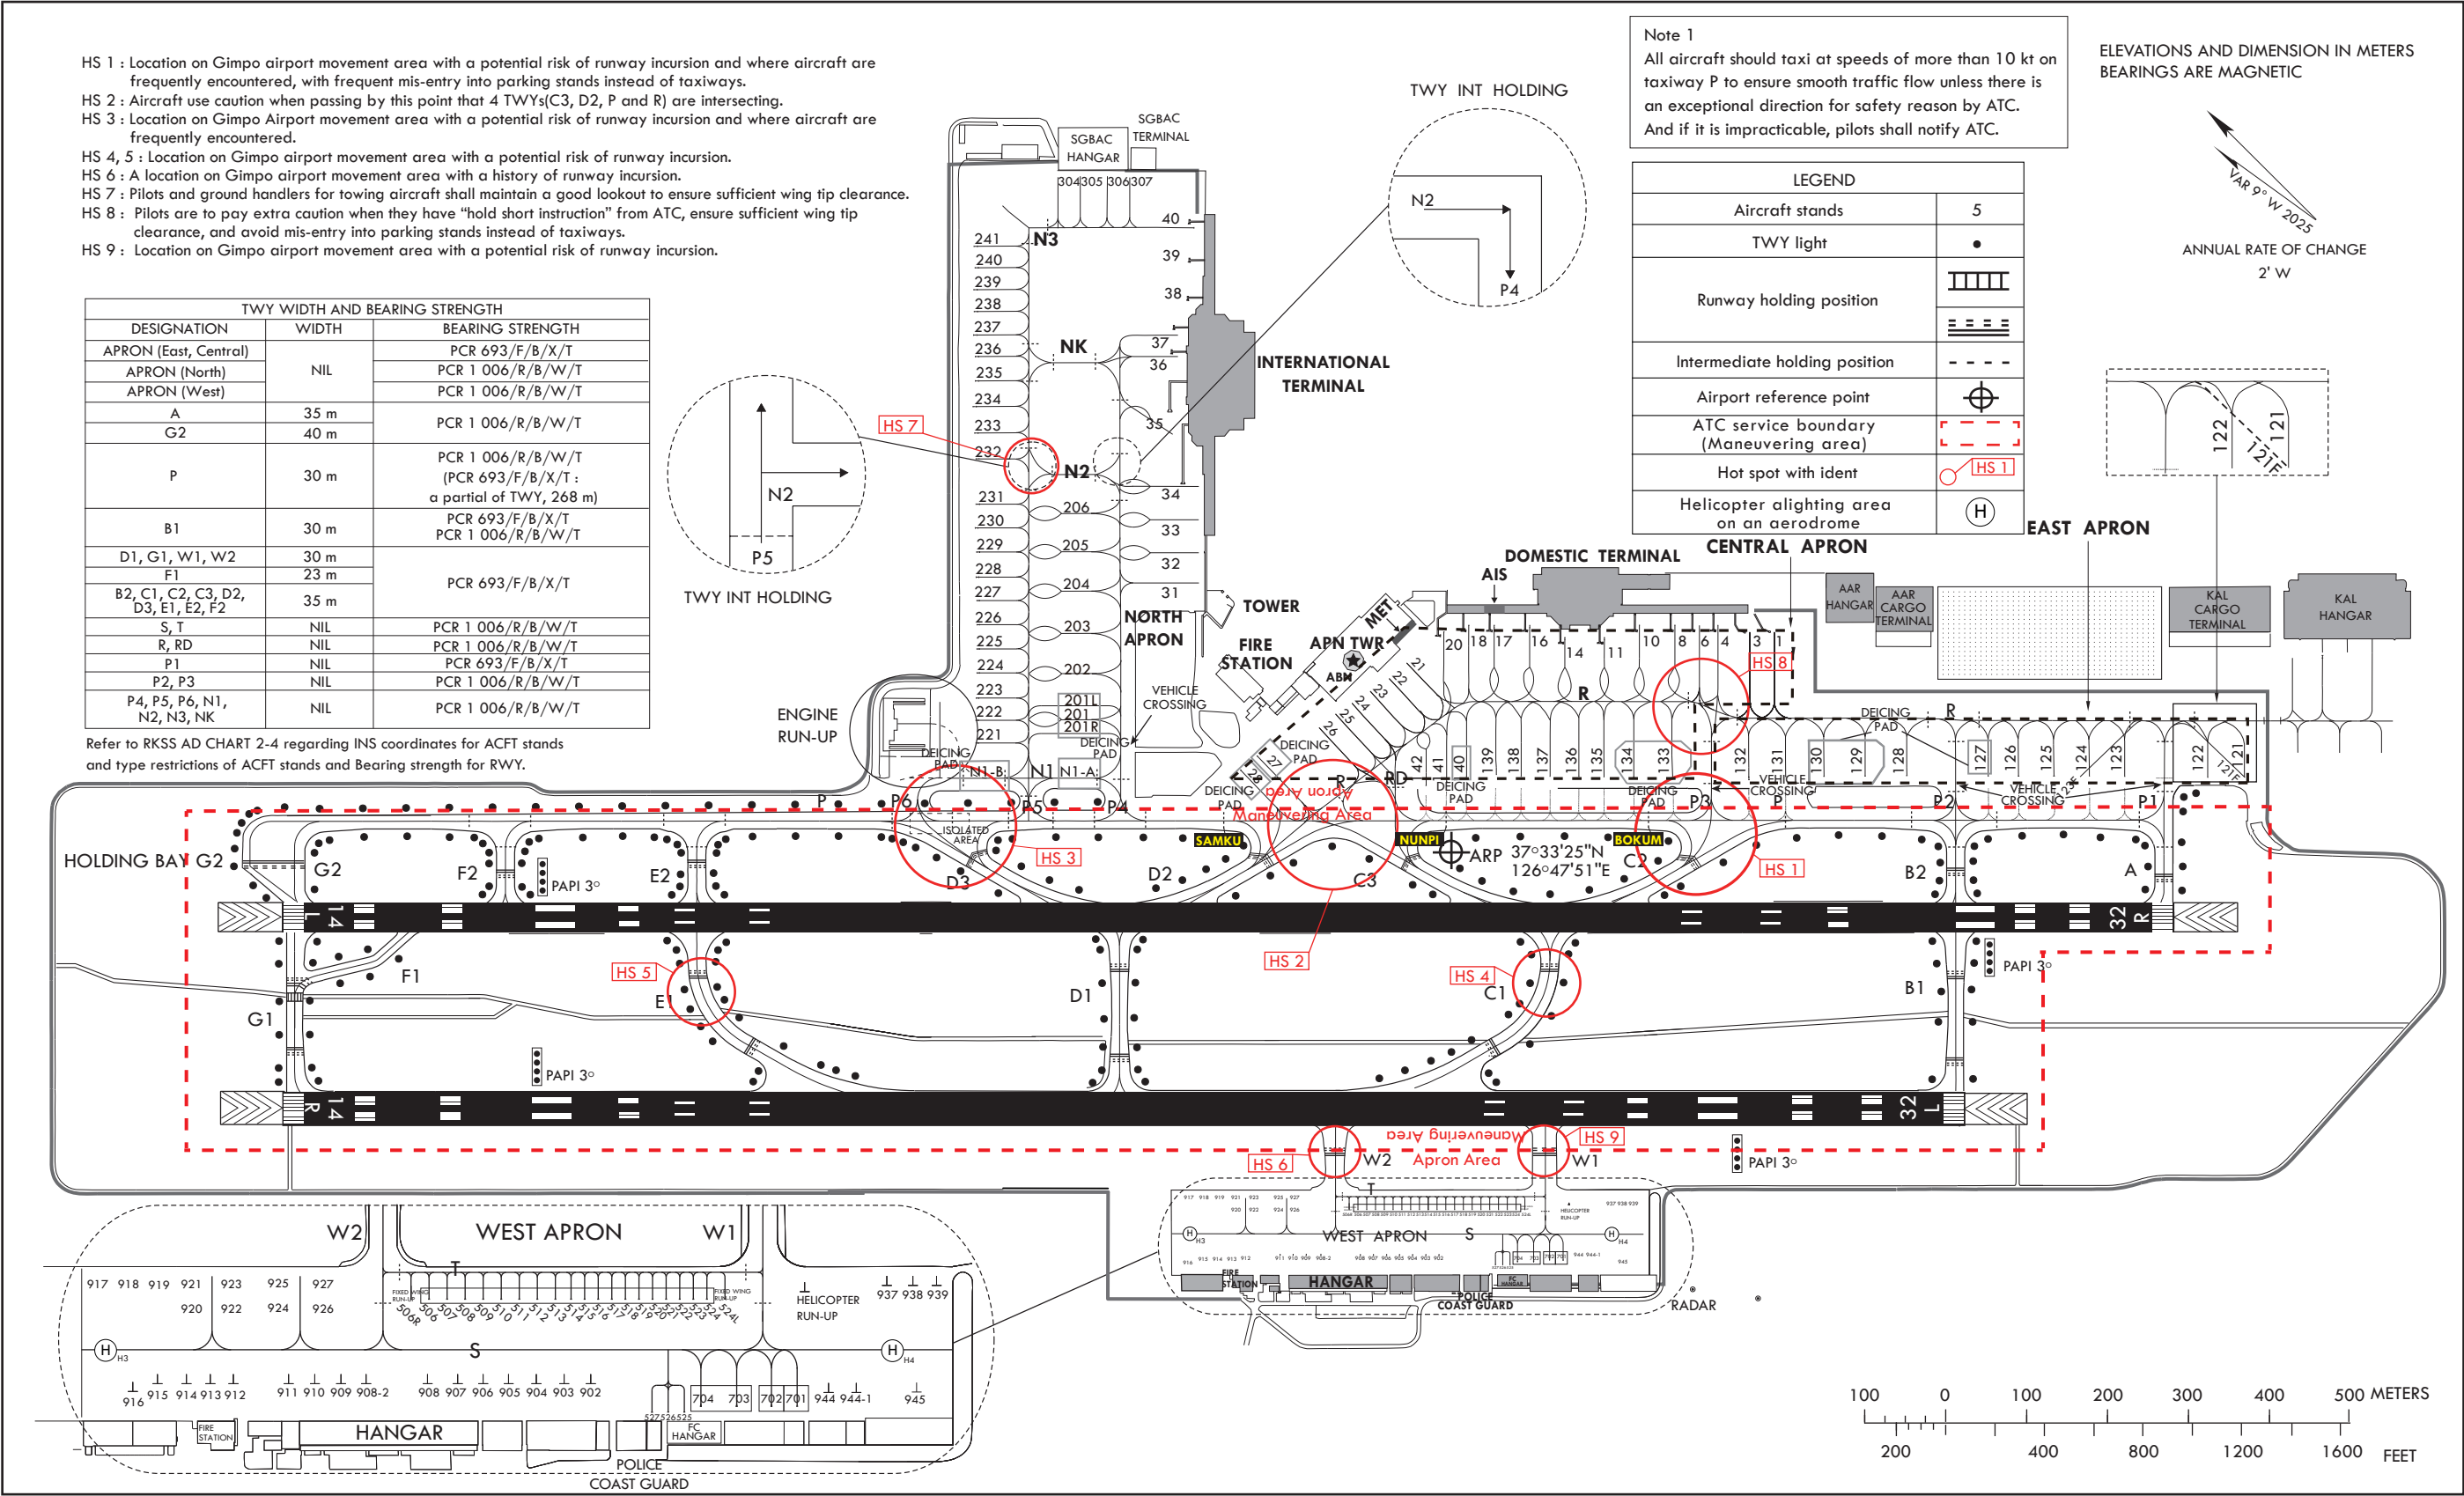

Change : Amended taxilane, ACFT stands and intermediate holding positions for north apron.

INS COORDINATES FOR AIRCRAFT STANDS (WGS-84)					
STAND NR	COORDINATES		STAND NR	COORDINATES	
1	37°33'21.66"N	126°48'19.06"E	202	37°33'50.75"N	126°47'39.70"E
3	37°33'22.69"N	126°48'17.76"E	203	37°33'52.36"N	126°47'41.86"E
4	37°33'23.72"N	126°48'16.46"E	204	37°33'54.02"N	126°47'43.95"E
6	37°33'24.75"N	126°48'15.17"E	205	37°33'55.68"N	126°47'46.38"E
8	37°33'26.37"N	126°48'13.90"E	206	37°33'57.40"N	126°47'48.06"E
10	37°33'28.03"N	126°48'11.82"E	221	37°33'52.40"N	126°47'30.17"E
11	37°33'28.80"N	126°48'09.44"E	222	37°33'53.40"N	126°47'31.43"E
14	37°33'30.53"N	126°48'07.28"E	223	37°33'54.40"N	126°47'32.68"E
16	37°33'32.62"N	126°48'06.03"E	224	37°33'55.34"N	126°47'34.10"E
17	37°33'34.16"N	126°48'03.89"E	225	37°33'56.34"N	126°47'35.26"E
18	37°33'35.37"N	126°48'02.21"E	226	37°33'57.34"N	126°47'36.51"E
20	37°33'36.05"N	126°48'00.62"E	227	37°33'58.34"N	126°47'37.76"E
21	37°33'36.23"N	126°47'57.36"E	228	37°33'59.33"N	126°47'39.14"E
22	37°33'36.31"N	126°47'55.39"E	229	37°34'00.33"N	126°47'40.27"E
23	37°33'36.33"N	126°47'53.74"E	230	37°34'01.33"N	126°47'41.52"E
24	37°33'36.41"N	126°47'52.04"E	231	37°34'02.33"N	126°47'42.77"E
25	37°33'36.98"N	126°47'50.47"E	232	37°34'04.42"N	126°47'45.40"E
26	37°33'37.59"N	126°47'48.82"E	233	37°34'05.42"N	126°47'46.66"E
27	37°33'39.32"N	126°47'44.18"E	234	37°34'06.46"N	126°47'47.84"E
28	37°33'39.15"N	126°47'42.44"E	235	37°34'07.46"N	126°47'49.97"E
31	37°33'49.67"N	126°47'49.76"E	236	37°34'08.46"N	126°47'50.35"E
32	37°33'51.06"N	126°47'51.46"E	237	37°34'09.46"N	126°47'51.60"E
33	37°33'52.80"N	126°47'53.65"E	238	37°34'10.45"N	126°47'52.85"E
34	37°33'54.54"N	126°47'55.84"E	239	37°34'11.45"N	126°47'54.11"E
35	37°33'57.13"N	126°47'57.80"E	240	37°34'12.45"N	126°47'55.36"E
36	37°33'59.84"N	126°48'01.16"E	241	37°34'13.45"N	126°47'56.61"E
37	37°34'00.77"N	126°48'02.33"E	304	37°34'13.71"N	126°48'05.17"E
38	37°34'01.89"N	126°48'05.36"E	305	37°34'12.14"N	126°48'06.34"E
39	37°34'03.46"N	126°48'07.50"E	306	37°34'11.15"N	126°48'07.76"E
40	37°34'05.14"N	126°48'09.63"E	307	37°34'10.69"N	126°48'08.92"E
121	37°32'55.01"N	126°48'37.35"E	506	37°33'14.76"N	126°47'24.92"E
121F	37°32'54.94"N	126°48'37.21"E	507	37°33'14.32"N	126°47'25.46"E
122	37°32'56.61"N	126°48'35.34"E	508	37°33'13.88"N	126°47'26.01"E
123	37°33'00.19"N	126°48'30.72"E	509	37°33'13.45"N	126°47'26.56"E
123F	37°33'01.94"N	126°48'28.35"E	510	37°33'13.01"N	126°47'27.11"E
124	37°33'01.72"N	126°48'28.74"E	511	37°33'12.57"N	126°47'27.66"E
125	37°33'03.25"N	126°48'26.78"E	512	37°33'12.14"N	126°47'28.20"E
126	37°33'04.80"N	126°48'24.83"E	513	37°33'11.72"N	126°47'28.75"E
127	37°33'06.03"N	126°48'23.26"E	514	37°33'11.29"N	126°47'29.28"E
128	37°33'09.73"N	126°48'18.72"E	515	37°33'10.91"N	126°47'29.76"E
129	37°33'11.55"N	126°48'16.44"E	516	37°33'10.59"N	126°47'30.16"E
130	37°33'13.42"N	126°48'14.14"E	517	37°33'10.27"N	126°47'30.57"E
131	37°33'14.99"N	126°48'12.01"E	518	37°33'09.95"N	126°47'30.97"E
132	37°33'16.61"N	126°48'10.05"E	519	37°33'09.63"N	126°47'31.38"E
133	37°33'19.96"N	126°48'05.76"E	520	37°33'09.31"N	126°47'31.78"E
134	37°33'21.63"N	126°48'03.67"E	521	37°33'08.99"N	126°47'32.18"E
135	37°33'22.97"N	126°48'02.00"E	522	37°33'08.67"N	126°47'32.59"E
136	37°33'24.37"N	126°48'00.31"E	523	37°33'08.35"N	126°47'32.99"E
137	37°33'25.52"N	126°47'58.89"E	524	37°33'08.03"N	126°47'33.40"E
138	37°33'26.65"N	126°47'57.44"E	525	37°33'06.65"N	126°47'28.93"E
139	37°33'27.66"N	126°47'56.39"E	526	37°33'06.97"N	126°47'28.53"E
140	37°33'28.81"N	126°47'54.72"E	527	37°33'07.29"N	126°47'28.13"E
141	37°33'29.57"N	126°47'53.35"E	701	37°33'04.09"N	126°47'32.21"E
142	37°33'30.47"N	126°47'52.15"E	702	37°33'04.79"N	126°47'31.35"E
201	37°33'48.61"N	126°47'37.13"E	703	37°33'05.63"N	126°47'30.20"E
201R	37°33'48.36"N	126°47'36.13"E	704	37°33'06.15"N	126°47'29.56"E
201L	37°33'49.37"N	126°47'37.40"E	902	37°33'08.81"N	126°47'27.24"E

RWY	DIRECTION (MAGNETIC)	THR (WGS-84)	BEARING STRENGTH
14R	144°	37°34'06"N 126°46'32"E	PCR 693/F/B/X/T Asphalt
32L	324°	37°32'53"N 126°48'04"E	
14L	144°	37°34'15"N 126°46'42"E	- PCR 693/F/B/X/T Asphalt - PCR 1 006/R/B/W/T Concrete (156 m from RWY THR)
32R	324°	37°32'52"N 126°48'26"E	- PCR 693/F/B/X/T Asphalt - PCR 1 006/R/B/W/T Concrete (151 m from RWY THR)
APRONS		East & Central	PCR 693/F/B/X/T
		North	PCR 1 006/R/B/W/T
		West	PCR 1 006/R/B/W/T

STANDS NUMBER	AIRCRAFT TYPE
121F, 123F	A380-800, B747-8
10, 16, 32, 33, 34, 38, 40, 133, 134, 201, 202, 203, 204, 205	B747-400, A340-600
35, 128, 129, 131	B747-400, A350-900
39	B777-300, A330-300
8, 17, 121, 124, 125, 132	B777-200, A330-300
14, 126, 130, 137, 206	B767-300
1, 3, 4, 6, 11, 18, 20, 21, 22, 23, 24, 25, 26, 27, 28, 31, 36, 37, 122, 123, 127, 135, 136, 138, 139, 140, 141, 142, 201R, 201L, 222, 223, 224, 225, 226, 227, 228, 229, 230, 231, 232, 233, 234, 235, 236, 237, 238, 239, 240, 241, 304, 305, 306, 307	B737MAX9, A321NEO
221	B737-900, A321-200

- * Code letter "D" and above aircraft are prohibited from taxiing out of all aircraft stands and performing forward towing operations.
- * Aircraft stands NR. 123-127, 131-142, 201-206 may be used by aircraft of ICAO code letter "C" or lower for self-maneuvering, subject to prior permission from ATC.
- * Taxiway intersection markings are provided for 5 places in front of the intersections / junctions on apron taxiway P4 and P5.
- * Isolated area : At the intersection of TWY D3 and TWY P.
- * De-icing pad : B737-800WL(MD-90) class ACFT - 27, 28, 140, 127 and 201L/R
B767 class ACFT - 130
B747 class ACFT - 129, 133, 134, 201 and N1-A, N1-B on the "N1" TWY
- * Engine Run-up : Front of "P6" TWY
- * Multiple Aircraft Ramp System(MARS) : 121F(121, 122), 123F(123, 124), 201L(201), 201R(201)

Aircraft Classification	Stand		Remarks
	Number	Dimensions(m)	
Helicopter	908-2, 902, 945	19×19	BELL214B-1
	903~908, 909~911	17.8×17.8	MI-2
	912~927, 944, 944-1	16×16	KA32-T
	937~939	15×15	EC-155B1
Fixed-wing	701, 702	25.8×21.4	CN235
	703, 704	20.86×19.61	CL-605
	515~527	9×11	C172R
	506~514	13×16	C-208B

* Dimensions means overall length × width

* Any Fixed-wing aircraft of wingspan exceed 16 m is prohibited to use Fixed-wing run up pad(524L/506R).

Change : Information of aircraft type for ACFT stands.