




MAGNETIC VARIATION 9° W-2025

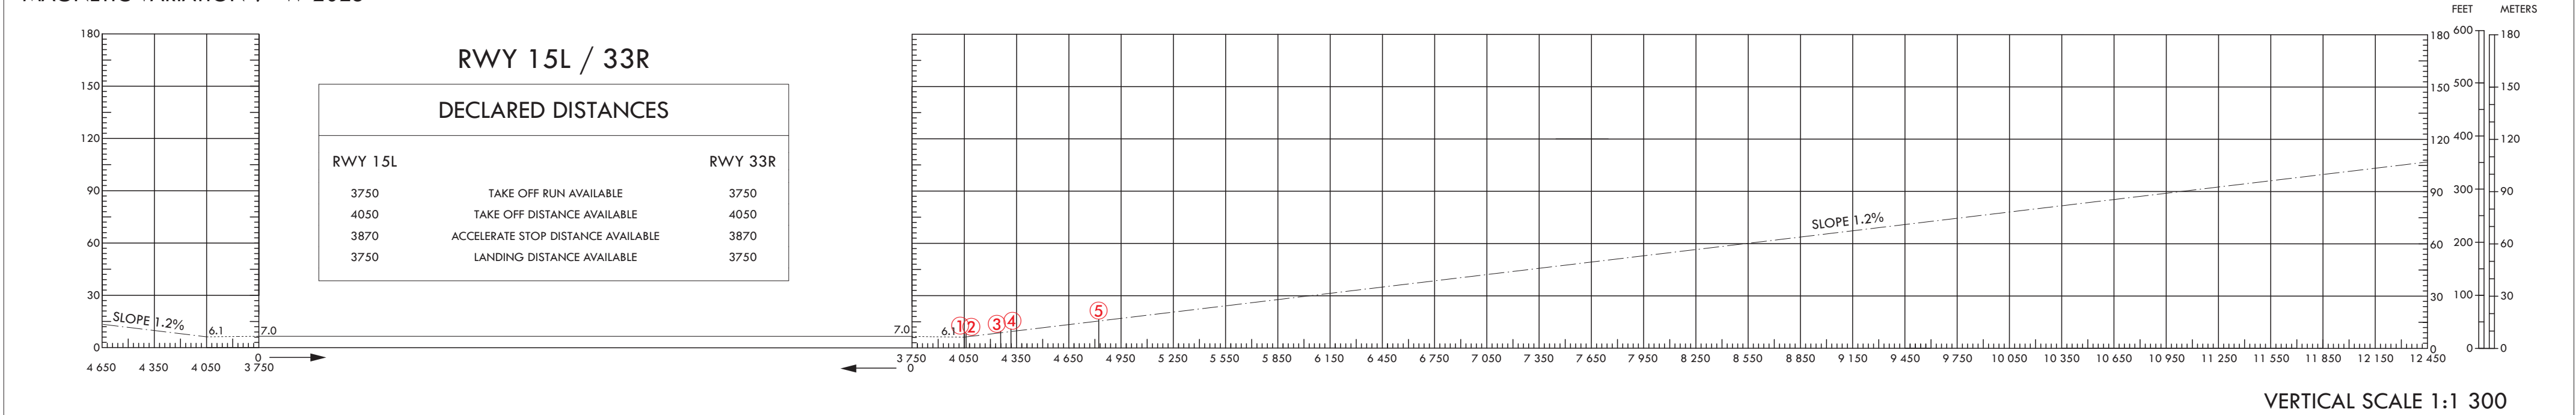


MAGNETIC VARIATION 9° W-2025

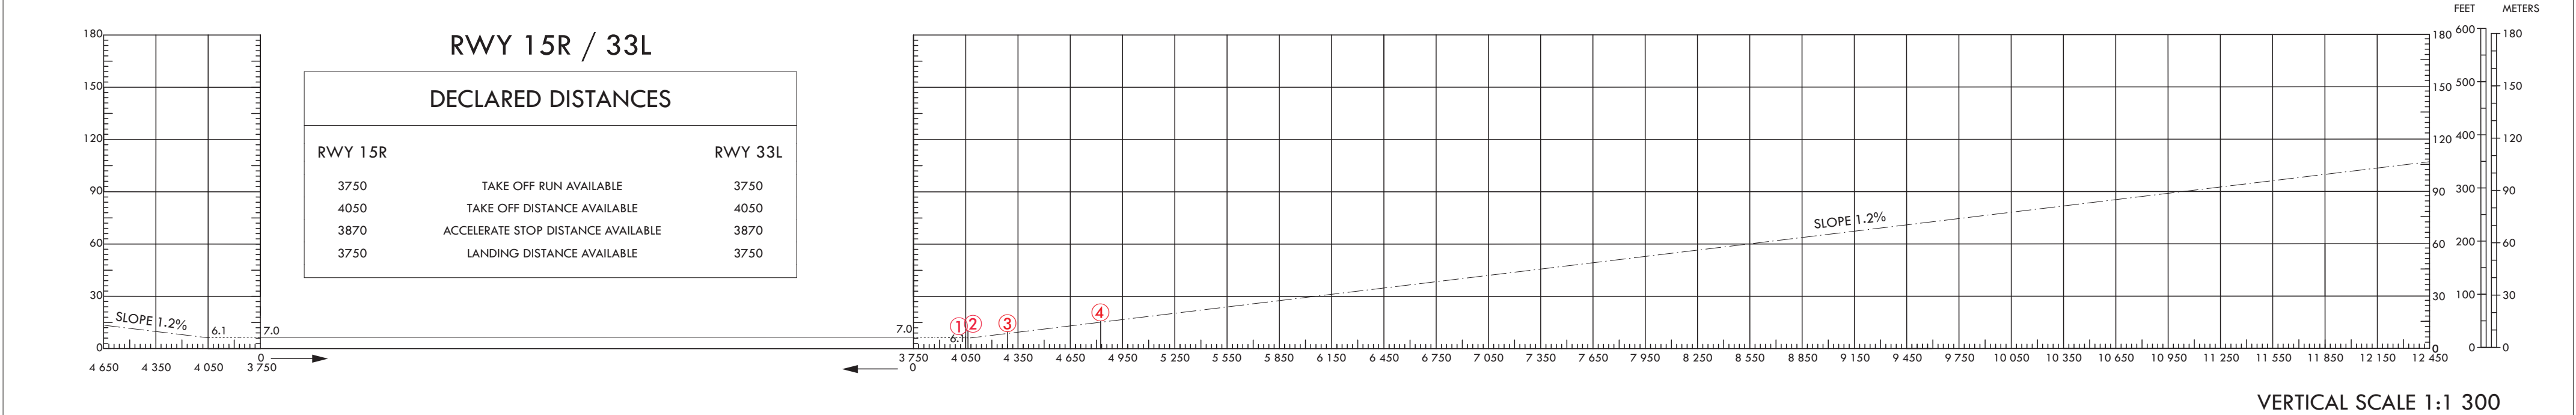

MAGNETIC VARIATION 9° W-2025

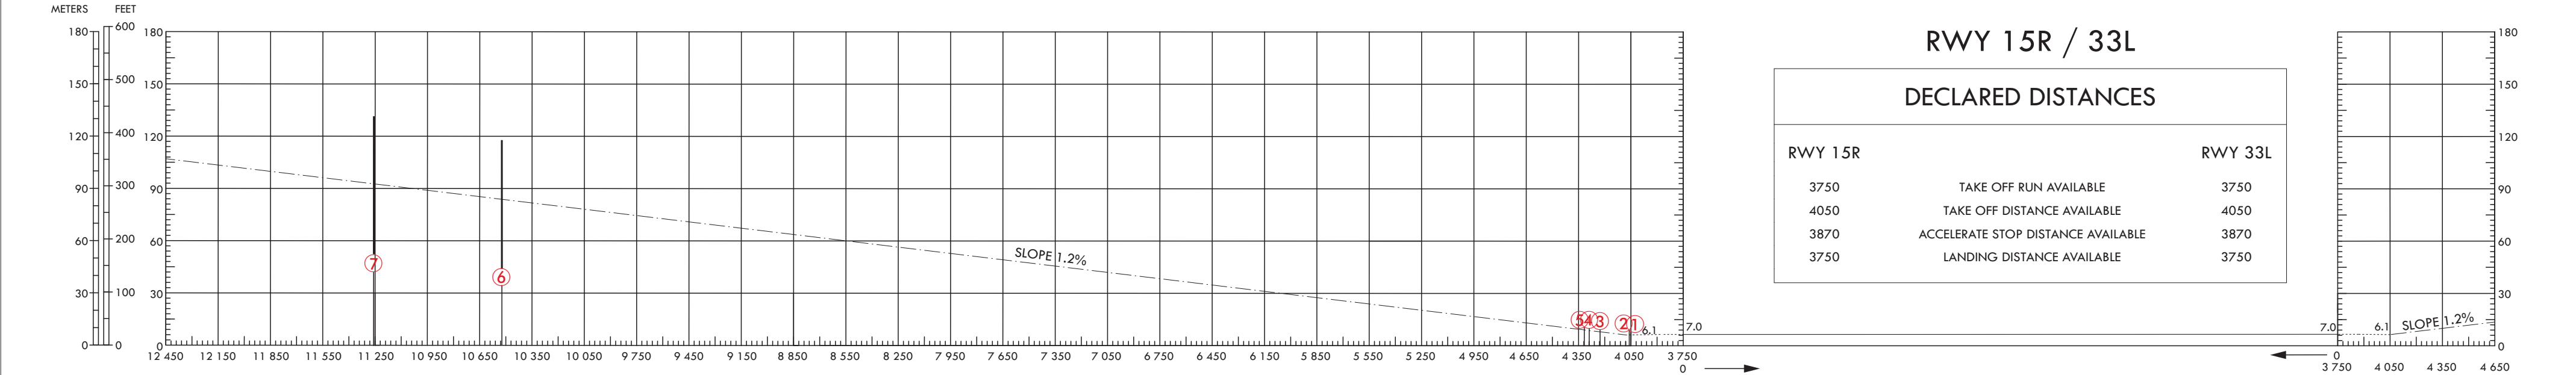

VERTICAL SCALE 1:1 300

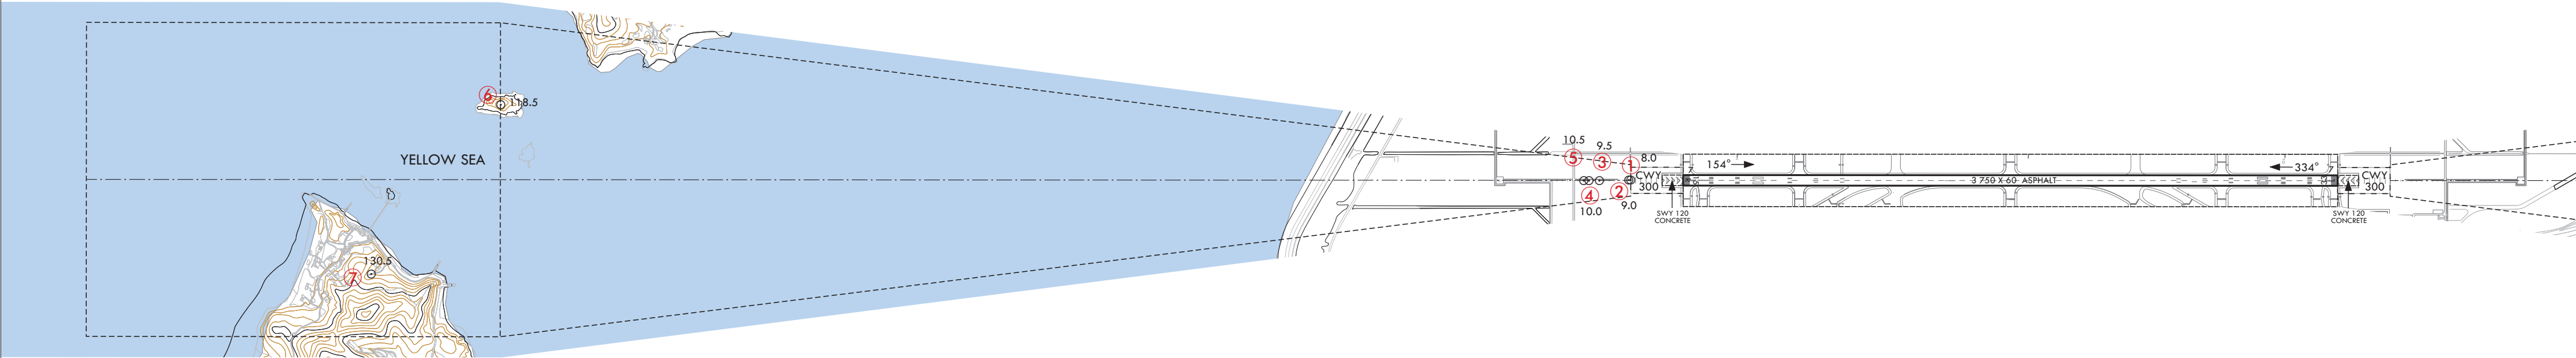


LEGEND		
ITEM	SYMBOL	
	Plan	Profile
Tree or shrub	✳	Identification number ○
Pole tower spire antenna etc	⊙	
Building or large structure	■	
Railroad	—+—+—+—	
Transmission line or overhead cable	—T—T—T—	
Natural High Point(Peak or Mountain)	●	 ○
Terrain penetrating obstacle plane	○	
Stopway(SWY)	□	
Clearway(CWY)	□	

OBSTACLES					
NR	COORDINATES(WGS-84)		ELEV(AMSL)	ITEM	NOTE
1	37°29'02.4"N	126°26'03.8"E	8.0	Light	
2	37°29'02.7"N	126°26'03.5"E	9.0	Antenna	
3	37°29'07.1"N	126°25'59.5"E	9.5	Light	
4	37°29'08.7"N	126°25'58.1"E	10.0	Light	
5	37°29'09.5"N	126°25'57.4"E	10.5	Light	
6	37°32'01.7"N	126°23'45.5"E	119.0	Tower	
7	37°32'03.9"N	126°22'55.8"E	130.5	Tower	

ORDER OF ACCURACY


HORIZONTAL 5.0 m
VERTICAL 0.5 m

HORIZONTAL SCALE 1 : 13 000

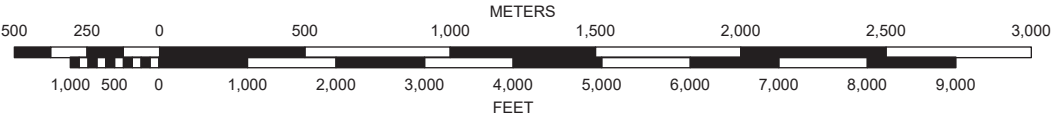



AMENDMENT RECORD		
NR.	DATE	ENTERED BY

AMENDMENT RECORD		
NR.	DATE	ENTERED BY

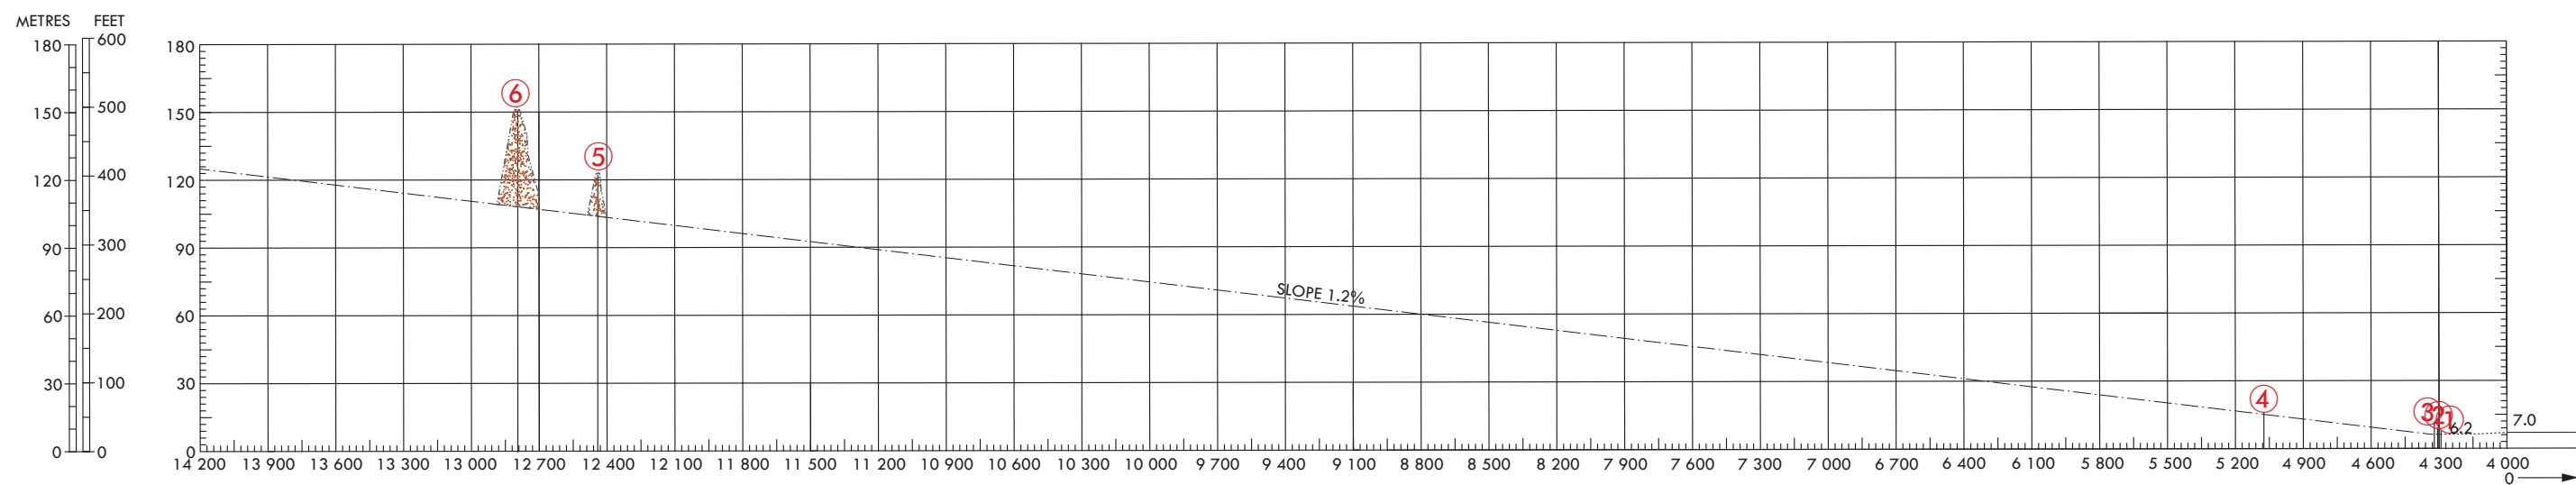

RWY 16L / 34R


DECLARED DISTANCES		
RWY 16L		RWY 34R
4000	TAKE OFF RUN AVAILABLE	4000
4300	TAKE OFF DISTANCE AVAILABLE	4300
4120	ACCELERATE STOP DISTANCE AVAILABLE	4120
4000	LANDING DISTANCE AVAILABLE	4000

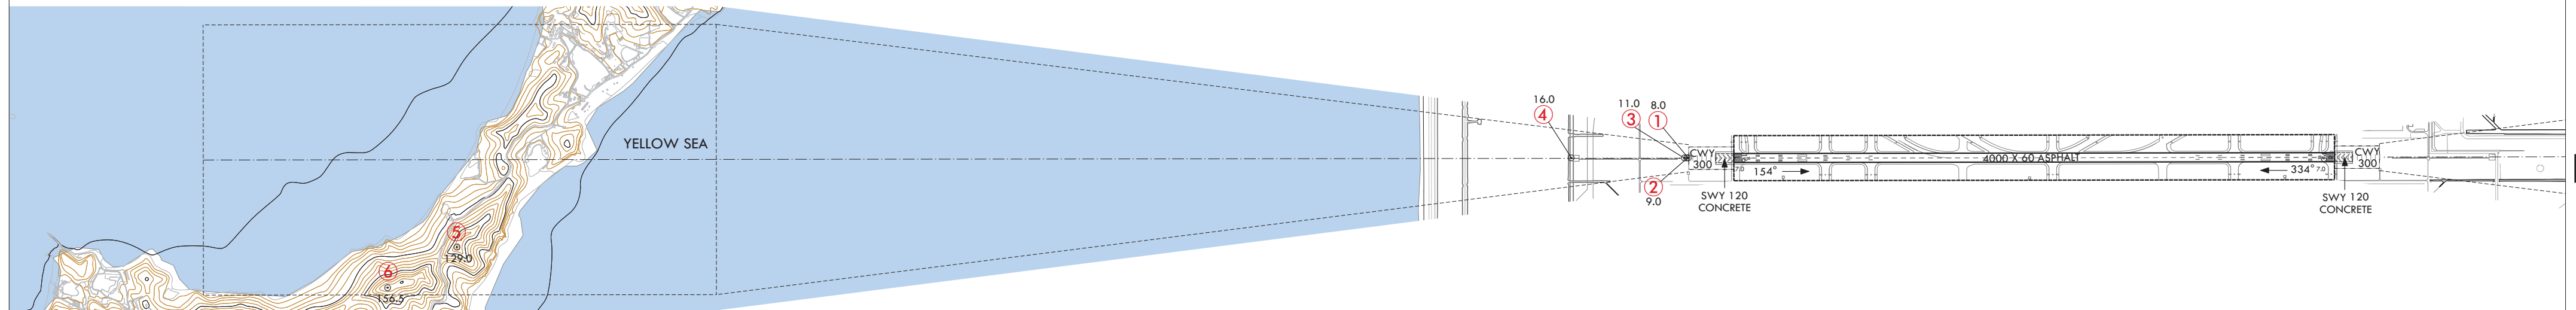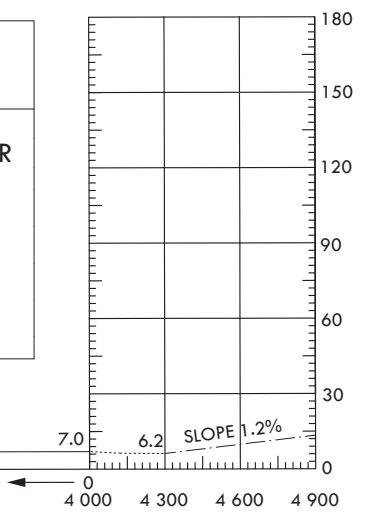

LEGEND		
ITEM	SYMBOL	
	Plan	Profile
Tree or shrub		
Pole tower spire antenna etc		
Building or large structure		
Railroad		
Transmission line or overhead cable		
Natural High Point(Peak or Mountain)		
Terrain penetrating obstacle plane		
Stopway(SWY)		
Clearway(CWY)		


OBSTACLES					
NR	COORDINATES(WGS-84)		ELEV(AMSL)	ITEM	NOTE
1	37°28'30.1"N	126°24'48.9"E	8.0	Light	
2	37°28'30.3"N	126°24'48.7"E	9.0	Antenna	
3	37°28'30.8"N	126°24'48.3"E	11.0	Antenna	
4	37°28'50.7"N	126°24'30.6"E	16.0	CCTV	
5	37°31'56.1"N	126°21'16.3"E	129.0	Natural high Point	
6	37°32'03.2"N	126°20'56.5"E	156.5	Natural high Point	


HORIZONTAL	5.0 m
VERTICAL	0.5 m

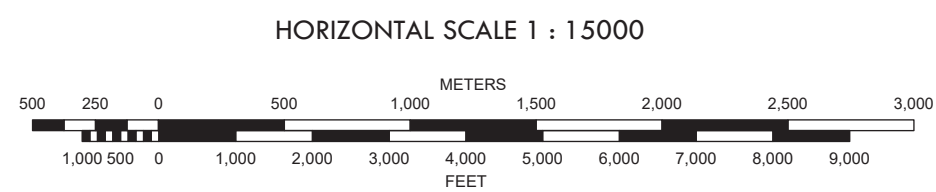

AMENDMENT RECORD		
NR.	DATE	ENTERED BY

MAGNETIC VARIATION 9° W-2025

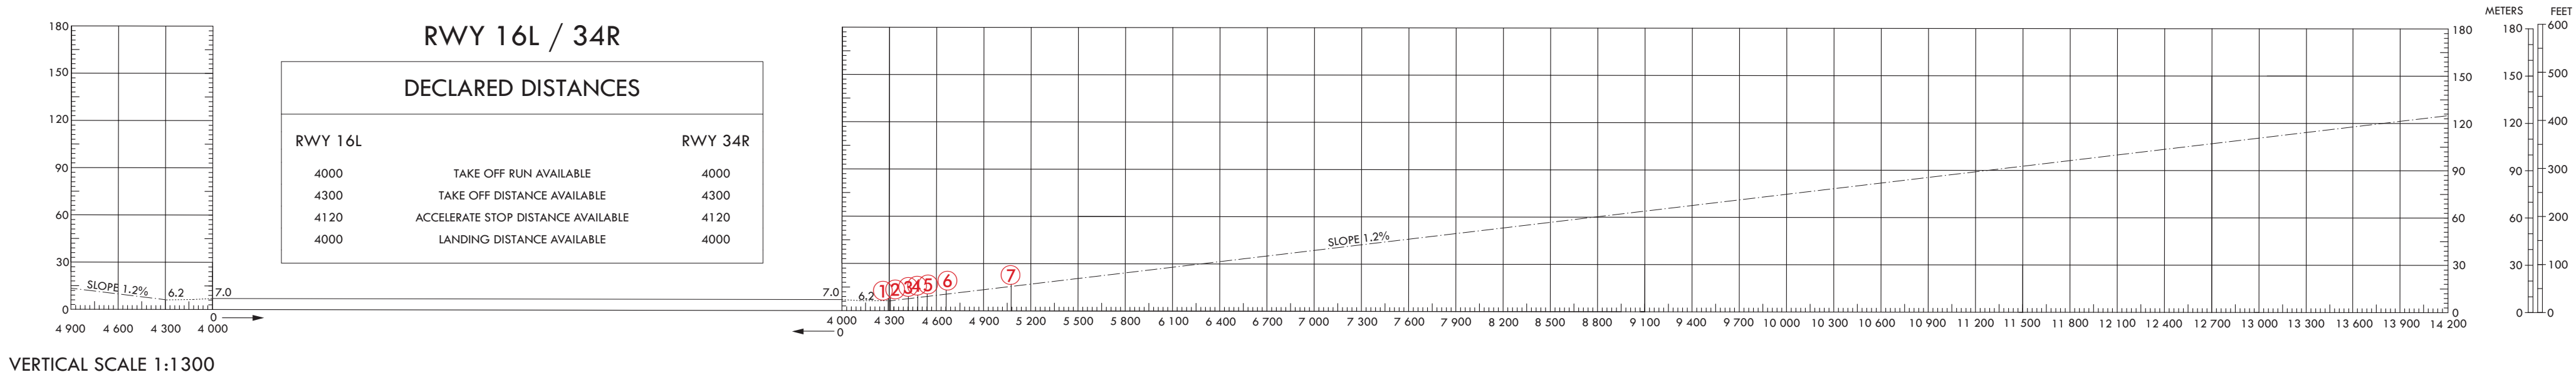

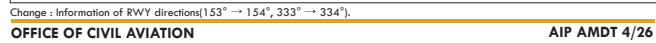

MAGNETIC VARIATION 9° W-2025

