AERODROME CHART - ICAO

37°33'25"N
126°47'51"E

ELEV **18** m

TWR	118.05	118.1	240.9
GND	121.9	121.95	
APN	129.525	130.875	131.175

SEOUL / Gimpo INTL

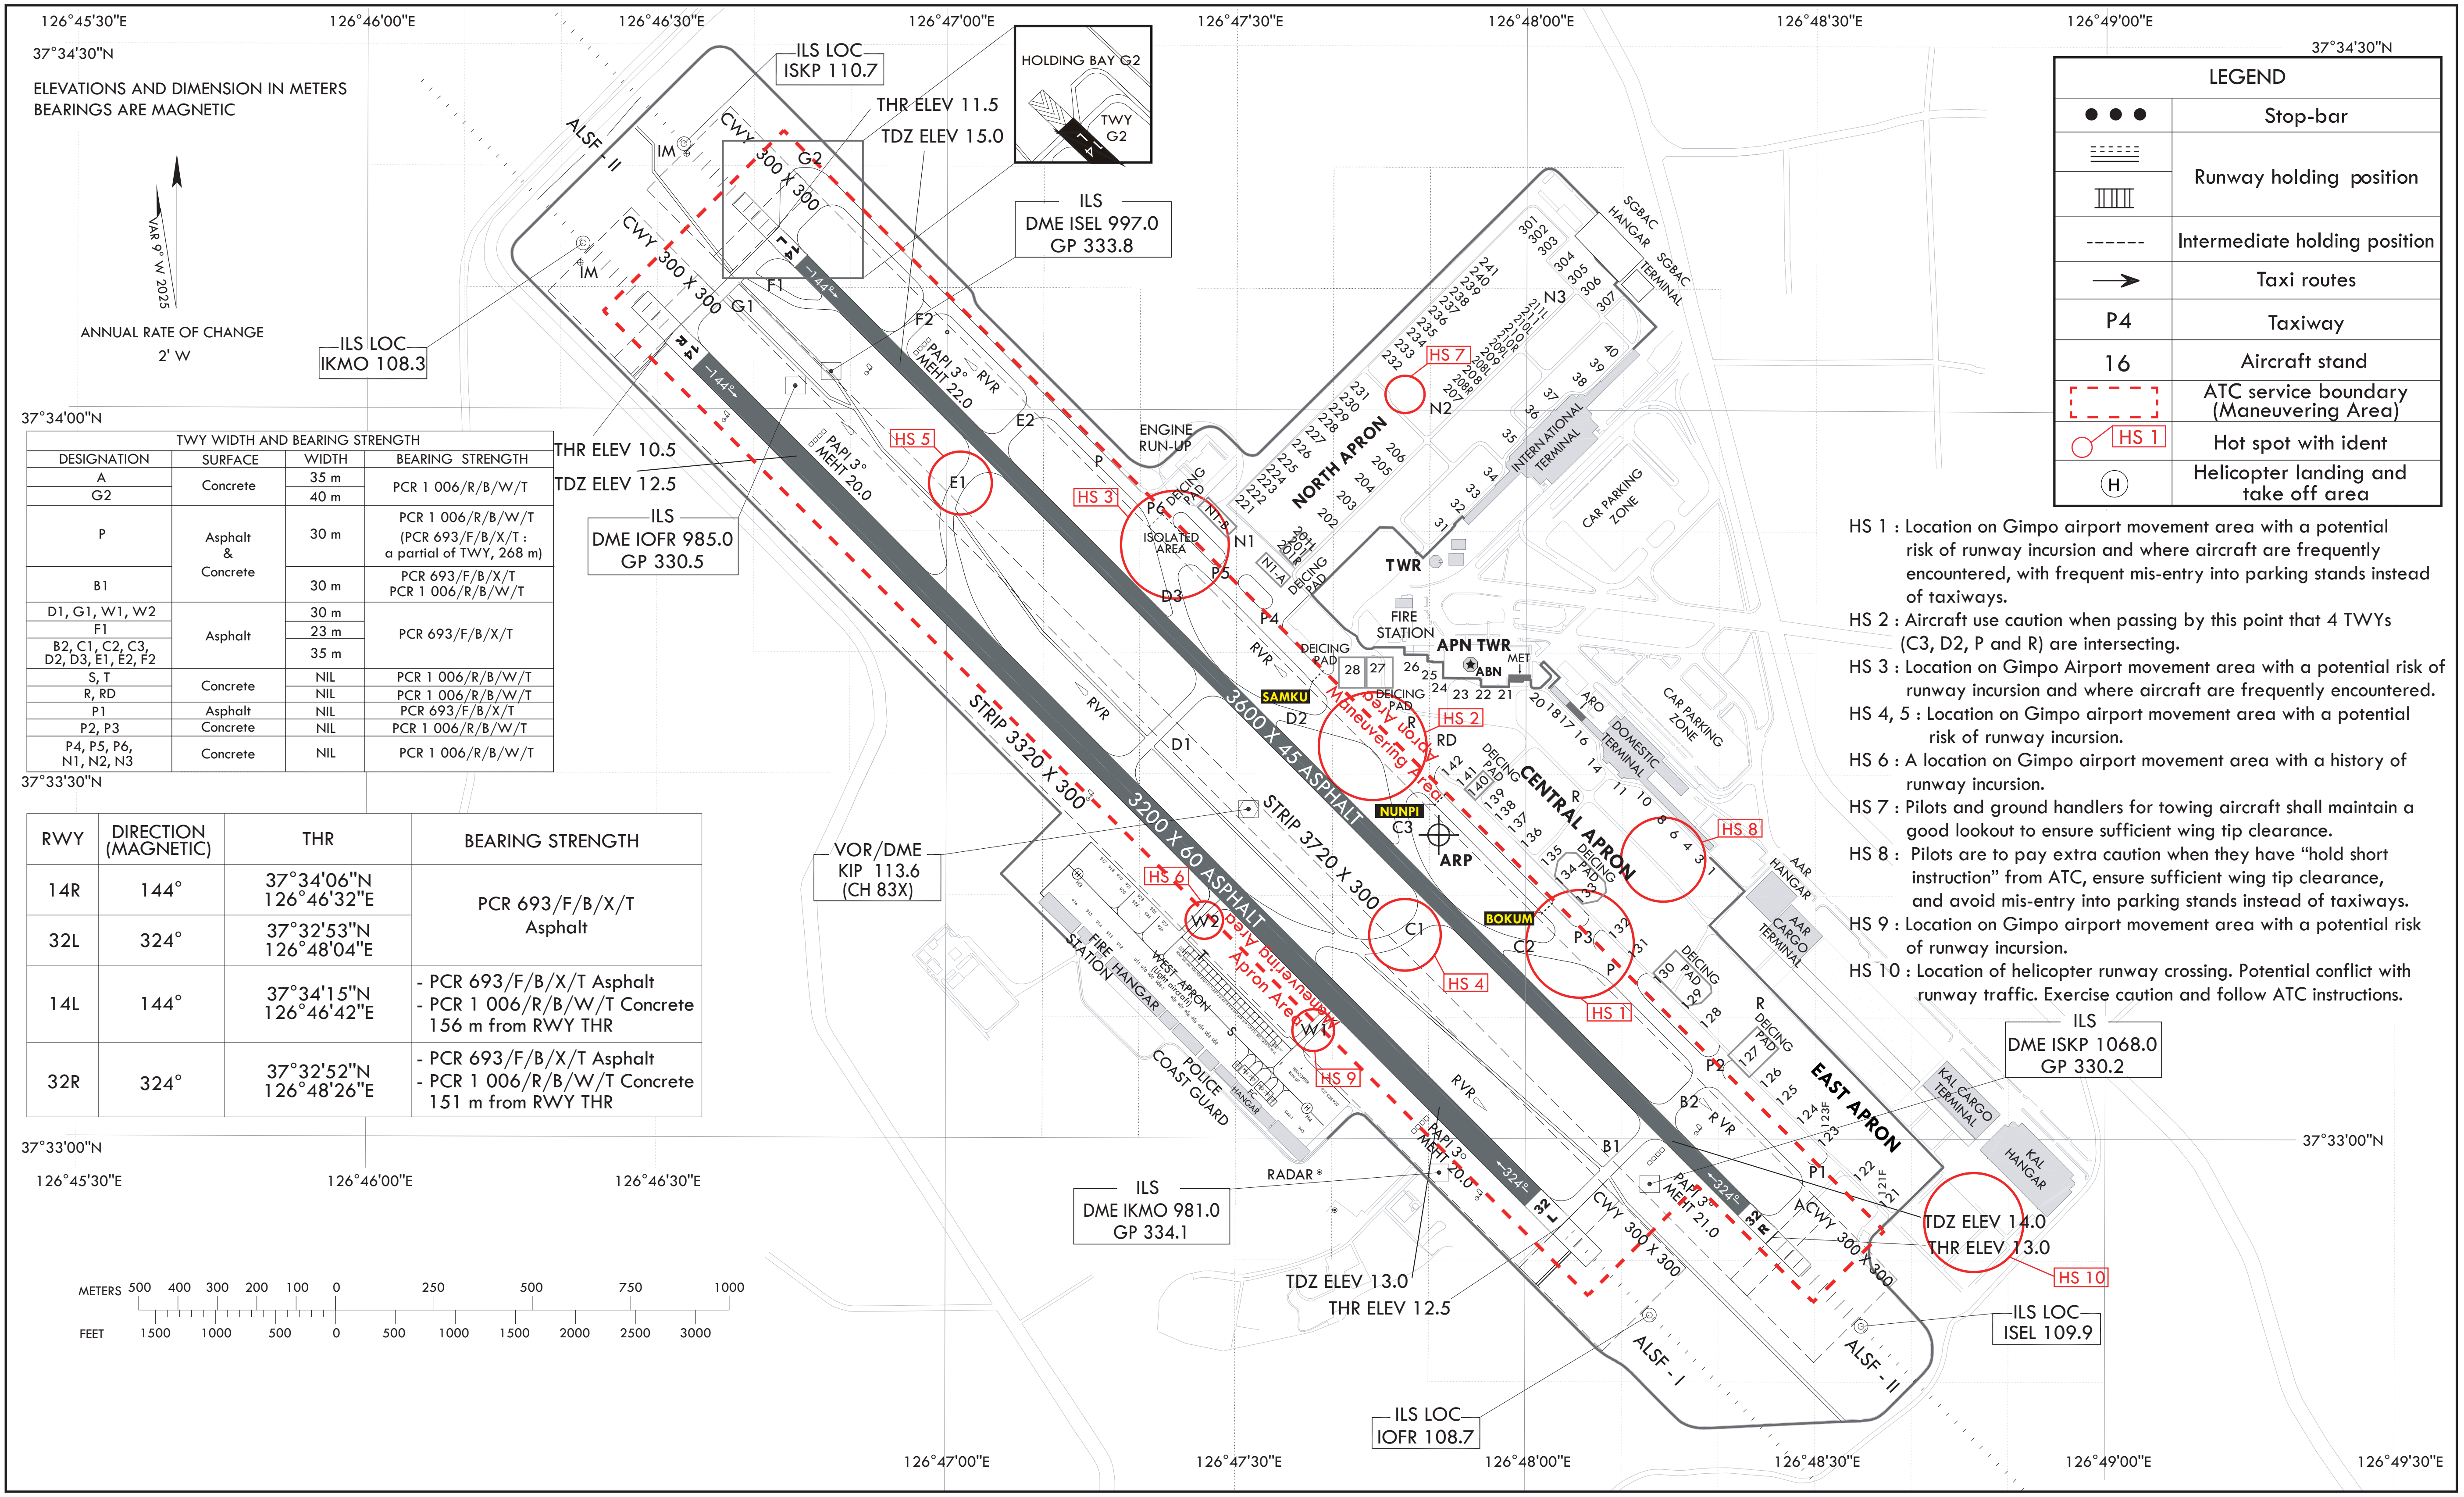
126°45'30"E
126°46'00"E
126°46'30"E
126°47'00"E
126°47'30"E
126°48'00"E
126°48'30"E
126°49'00"E
126°49'30"E
37°34'30"N
37°34'00"N
37°33'30"N
37°33'00"N
ELEVATIONS AND DIMENSION IN METERS
BEARINGS ARE MAGNETIC
VAR 9° W 2025
ANNUAL RATE OF CHANGE
2' W
ILS LOC
ISKP 110.7
THR ELEV 11.5
TDZ ELEV 15.0
HOLDING BAY G2
TWY G2
ILS
DME ISEL 997.0
GP 333.8
ALSF - II
IM
CWY 300 X 300
G2
F1
G1
F2
PAPI 3°
MEHT 22.0
RVR
E2
ILS LOC
IKMO 108.3
THR ELEV 10.5
TDZ ELEV 12.5
ILS
DME IOFR 985.0
GP 330.5
PAPI 3°
MEHT 20.0
HS 5
E1
ENGINE RUN-UP
P
HS 3
DEICING PAD
P6
ISOLATED AREA
N1
N1-A
D3
P5
P4
HS 7
N2
N3
NORTH APRON
SGBAC HANGAR
SGBAC TERMINAL
INTERNATIONAL TERMINAL
CAR PARKING ZONE
TWR
FIRE STATION
APN TWR
ABN
MET
SAMKU
D2
HS 2
RD
R
Heavy Aircraft Maneuvering Area
ARO
DOMESTIC TERMINAL
CAR PARKING ZONE
CENTRAL APRON
HS 8
NUNPI
C3
ARP
D1
3600 X 45 ASPHALT
STRIP 3720 X 300
STRIP 3320 X 300
3200 X 60 ASPHALT
VOR/DME
KIP 113.6
(CH 83X)
HS 6
W2
Heavy Aircraft Maneuvering Area
Apron Area
W1
HS 9
WEST APRON
FIRE STATION
HANGAR
POLICE
COAST GUARD
T
S
C1
HS 4
BOKUM
C2
P3
HS 1
AAR HANGAR
AAR CARGO TERMINAL
EAST APRON
P2
B2
RVR
B1
P1
ILS
DME ISKP 1068.0
GP 330.2
KAL CARGO TERMINAL
KAL HANGAR
RADAR
ILS
DME IKMO 981.0
GP 334.1
PAPI 3°
MEHT 20.0
PAPI 3°
MEHT 21.0
TDZ ELEV 13.0
THR ELEV 12.5
CWY 300 X 300
TDZ ELEV 14.0
THR ELEV 13.0
HS 10
ILS LOC
ISEL 109.9
ALSF - I
ALSF - II
ILS LOC
IOFR 108.7
144°
324°
METERS 500 400 300 200 100 0 250 500 750 1000
FEET 1500 1000 500 0 500 1000 1500 2000 2500 3000

TWY WIDTH AND BEARING STRENGTH			
DESIGNATION	SURFACE	WIDTH	BEARING STRENGTH
A	Concrete	35 m	PCR 1 006/R/B/W/T
G2		40 m	
P	Asphalt & Concrete	30 m	PCR 1 006/R/B/W/T (PCR 693/F/B/X/T : a partial of TWY, 268 m)
B1		30 m	PCR 693/F/B/X/T PCR 1 006/R/B/W/T
D1, G1, W1, W2	Asphalt	30 m	PCR 693/F/B/X/T
F1		23 m	
B2, C1, C2, C3, D2, D3, E1, E2, F2		35 m	
S, T	Concrete	NIL	PCR 1 006/R/B/W/T
R, RD		NIL	PCR 1 006/R/B/W/T
P1	Asphalt	NIL	PCR 693/F/B/X/T
P2, P3	Concrete	NIL	PCR 1 006/R/B/W/T
P4, P5, P6, N1, N2, N3	Concrete	NIL	PCR 1 006/R/B/W/T

RWY	DIRECTION (MAGNETIC)	THR	BEARING STRENGTH
14R	144°	37°34'06"N 126°46'32"E	PCR 693/F/B/X/T Asphalt
32L	324°	37°32'53"N 126°48'04"E	
14L	144°	37°34'15"N 126°46'42"E	- PCR 693/F/B/X/T Asphalt - PCR 1 006/R/B/W/T Concrete 156 m from RWY THR
32R	324°	37°32'52"N 126°48'26"E	- PCR 693/F/B/X/T Asphalt - PCR 1 006/R/B/W/T Concrete 151 m from RWY THR

LEGEND	
● ● ●	Stop-bar
▤	Runway holding position
------	Intermediate holding position
→	Taxi routes
P4	Taxiway
16	Aircraft stand
▭	ATC service boundary (Maneuvering Area)
○ HS 1	Hot spot with ident
Ⓗ	Helicopter landing and take off area

HS 1 : Location on Gimpo airport movement area with a potential risk of runway incursion and where aircraft are frequently encountered, with frequent mis-entry into parking stands instead of taxiways.

HS 2 : Aircraft use caution when passing by this point that 4 TWYs (C3, D2, P and R) are intersecting.

HS 3 : Location on Gimpo Airport movement area with a potential risk of runway incursion and where aircraft are frequently encountered.

HS 4, 5 : Location on Gimpo airport movement area with a potential risk of runway incursion.

HS 6 : A location on Gimpo airport movement area with a history of runway incursion.

HS 7 : Pilots and ground handlers for towing aircraft shall maintain a good lookout to ensure sufficient wing tip clearance.

HS 8 : Pilots are to pay extra caution when they have "hold short instruction" from ATC, ensure sufficient wing tip clearance, and avoid mis-entry into parking stands instead of taxiways.

HS 9 : Location on Gimpo airport movement area with a potential risk of runway incursion.

HS 10 : Location of helicopter runway crossing. Potential conflict with runway traffic. Exercise caution and follow ATC instructions.

Change : Amended THR coordinates of RWY 14R/L.

LIGHTING AND MARKING CHART

SEOUL / Gimpo INTL

LIGHTING AIDS RWY 14R/32L AND 14L/32R AND EXIT TWY

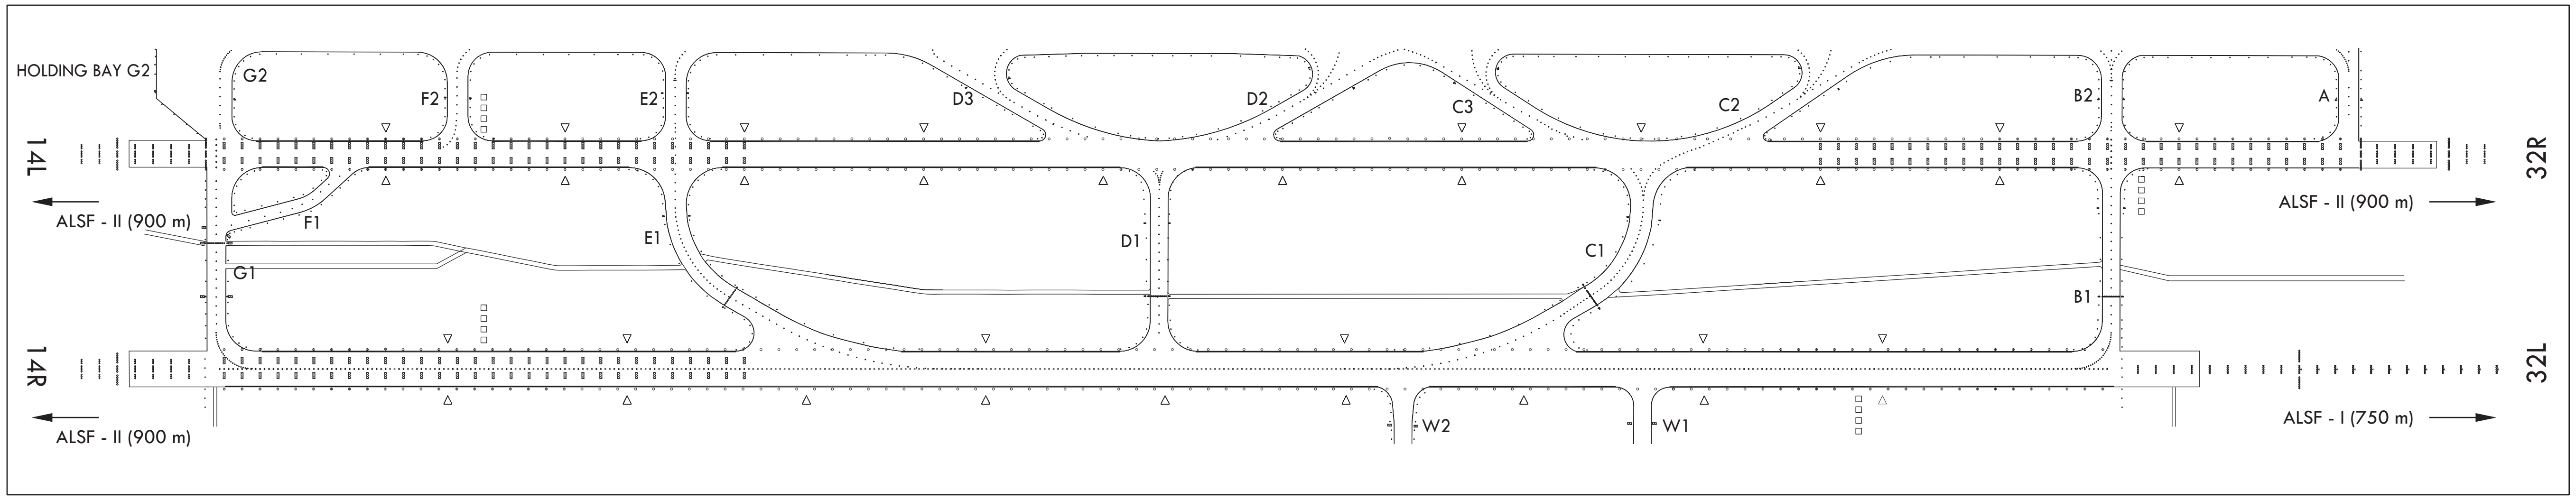
HOLDING BAY G2
G2
F2
E2
D3
D2
C3
C2
B2
A
14L
32R
ALSF - II (900 m)
F1
E1
D1
C1
G1
B1
ALSF - II (900 m)
14R
32L
W2
W1
ALSF - II (900 m)
ALSF - I (750 m)

MARKING AIDS RWY 14R/32L AND 14L/32R AND EXIT TWY

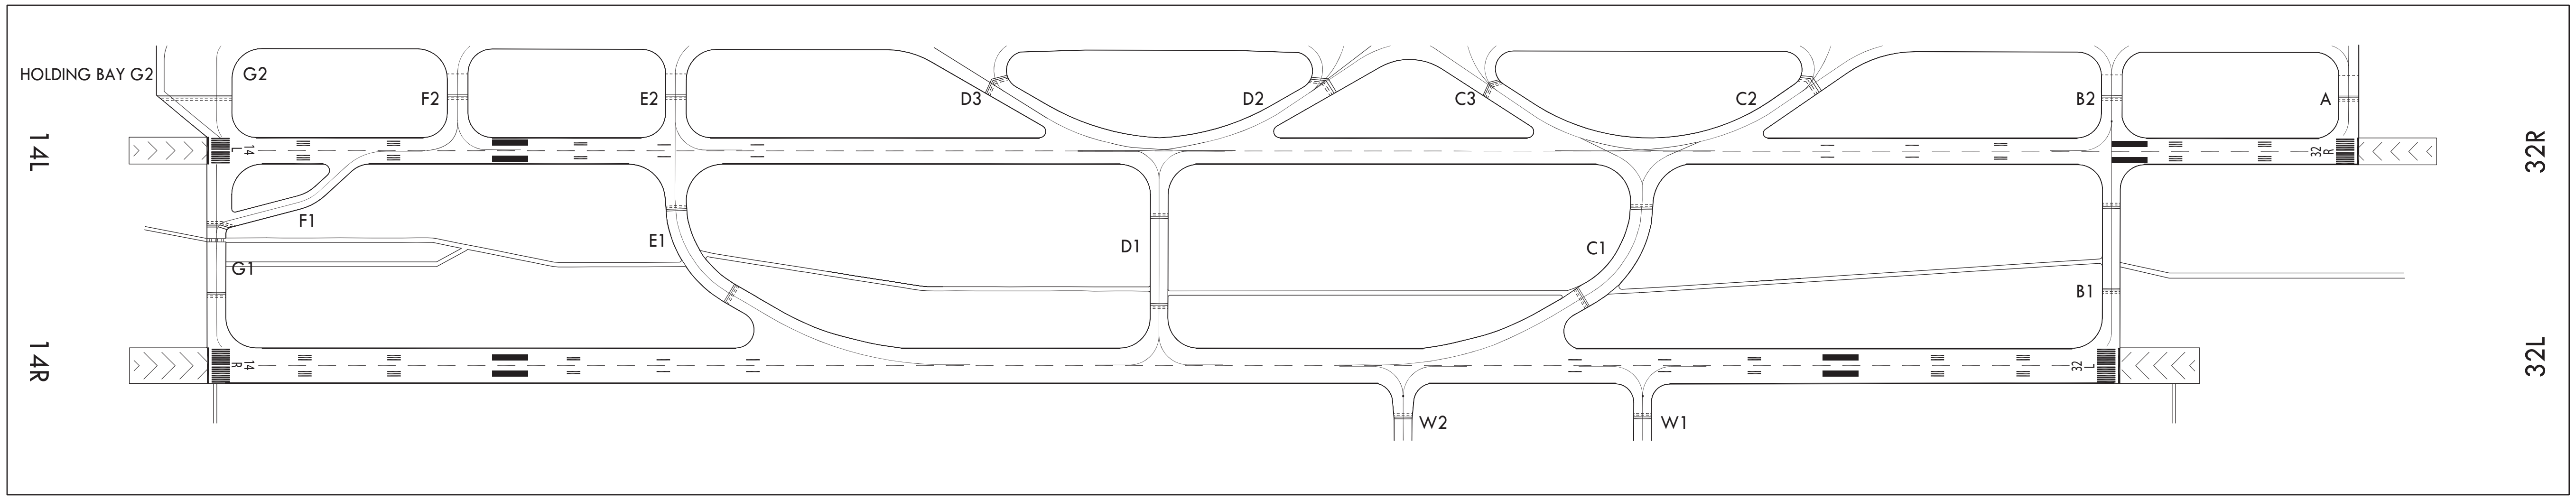
HOLDING BAY G2
G2
F2
E2
D3
D2
C3
C2
B2
A
14L
32R
F1
E1
D1
C1
G1
B1
14R
32L
W2
W1

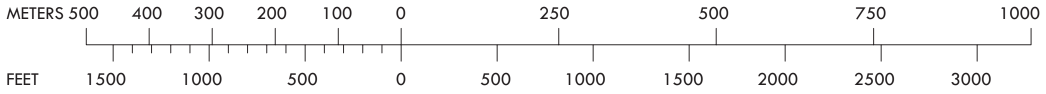
METERS 500
400
300
200
100
0
250
500
750
1000
FEET
1500
1000
500
0
500
1000
1500
2000
2500
3000