AIRCRAFT PARKING/ DOCKING CHART - ICAO

SEOUL / Gimpo INTL

APRON ELEV	
Central Apron	**16** m
The Other	**13** m

TWR	118.1
GND	121.9
APN	130.875

HS 1 : Location on Gimpo airport movement area with a potential risk of runway incursion and where aircraft are frequently encountered, with frequent mis-entry into parking stands instead of taxiways.
HS 2 : Aircraft use caution when passing by this point that 4 TWYs(C3, D2, P and R) are intersecting.
HS 3 : Location on Gimpo Airport movement area with a potential risk of runway incursion and where aircraft are frequently encountered.
HS 4, 5 : Location on Gimpo airport movement area with a potential risk of runway incursion.
HS 6 : A location on Gimpo airport movement area with a history of runway incursion.
HS 7 : Pilots and ground handlers for towing aircraft shall maintain a good lookout to ensure sufficient wing tip clearance.
HS 8 : Pilots are to pay extra caution when they have "hold short instruction" from ATC, ensure sufficient wing tip clearance, and avoid mis-entry into parking stands instead of taxiways.
HS 9 : Location on Gimpo airport movement area with a potential risk of runway incursion.
HS 10 : Location of helicopter runway crossing. Potential conflict with runway traffic. Exercise caution and follow ATC instructions.

TWY WIDTH AND BEARING STRENGTH		
DESIGNATION	WIDTH	BEARING STRENGTH
APRON (East, Central)	NIL	PCR 693/F/B/X/T PCR 1 006/R/B/W/T
APRON (North)		PCR 1 006/R/B/W/T
APRON (West)		PCR 1 006/R/B/W/T
A	35 m	PCR 1 006/R/B/W/T
G2	40 m	
P	30 m	PCR 1 006/R/B/W/T (PCR 693/F/B/X/T : a partial of TWY, 268 m)
B1	30 m	PCR 693/F/B/X/T PCR 1 006/R/B/W/T
D1, G1, W1, W2	30 m	PCR 693/F/B/X/T
F1	23 m	
B2, C1, C2, C3, D2, D3, E1, E2, F2	35 m	
S, T	NIL	PCR 1 006/R/B/W/T
R, RD	NIL	PCR 1 006/R/B/W/T
P1	NIL	PCR 693/F/B/X/T
P2, P3	NIL	PCR 1 006/R/B/W/T
P4, P5, P6, N1, N2, N3	NIL	PCR 1 006/R/B/W/T


Refer to RKSS AD CHART 2-4 regarding INS coordinates for ACFT stands and type restrictions of ACFT stands and Bearing strength for RWY.

Note 1
All aircraft should taxi at speeds of more than 10 kt on taxiway P to ensure smooth traffic flow unless there is an exceptional direction for safety reason by ATC.
And if it is impracticable, pilots shall notify ATC.

LEGEND	
Aircraft stands	5
TWY light	•
Runway holding position	
Intermediate holding position	
Airport reference point	
ATC service boundary (Maneuvering area)	
Hot spot with ident	HS 1
Helicopter alighting area on an aerodrome	H

ELEVATIONS AND DIMENSION IN METERS
BEARINGS ARE MAGNETIC

VAR 9° W 2025
ANNUAL RATE OF CHANGE 2' W

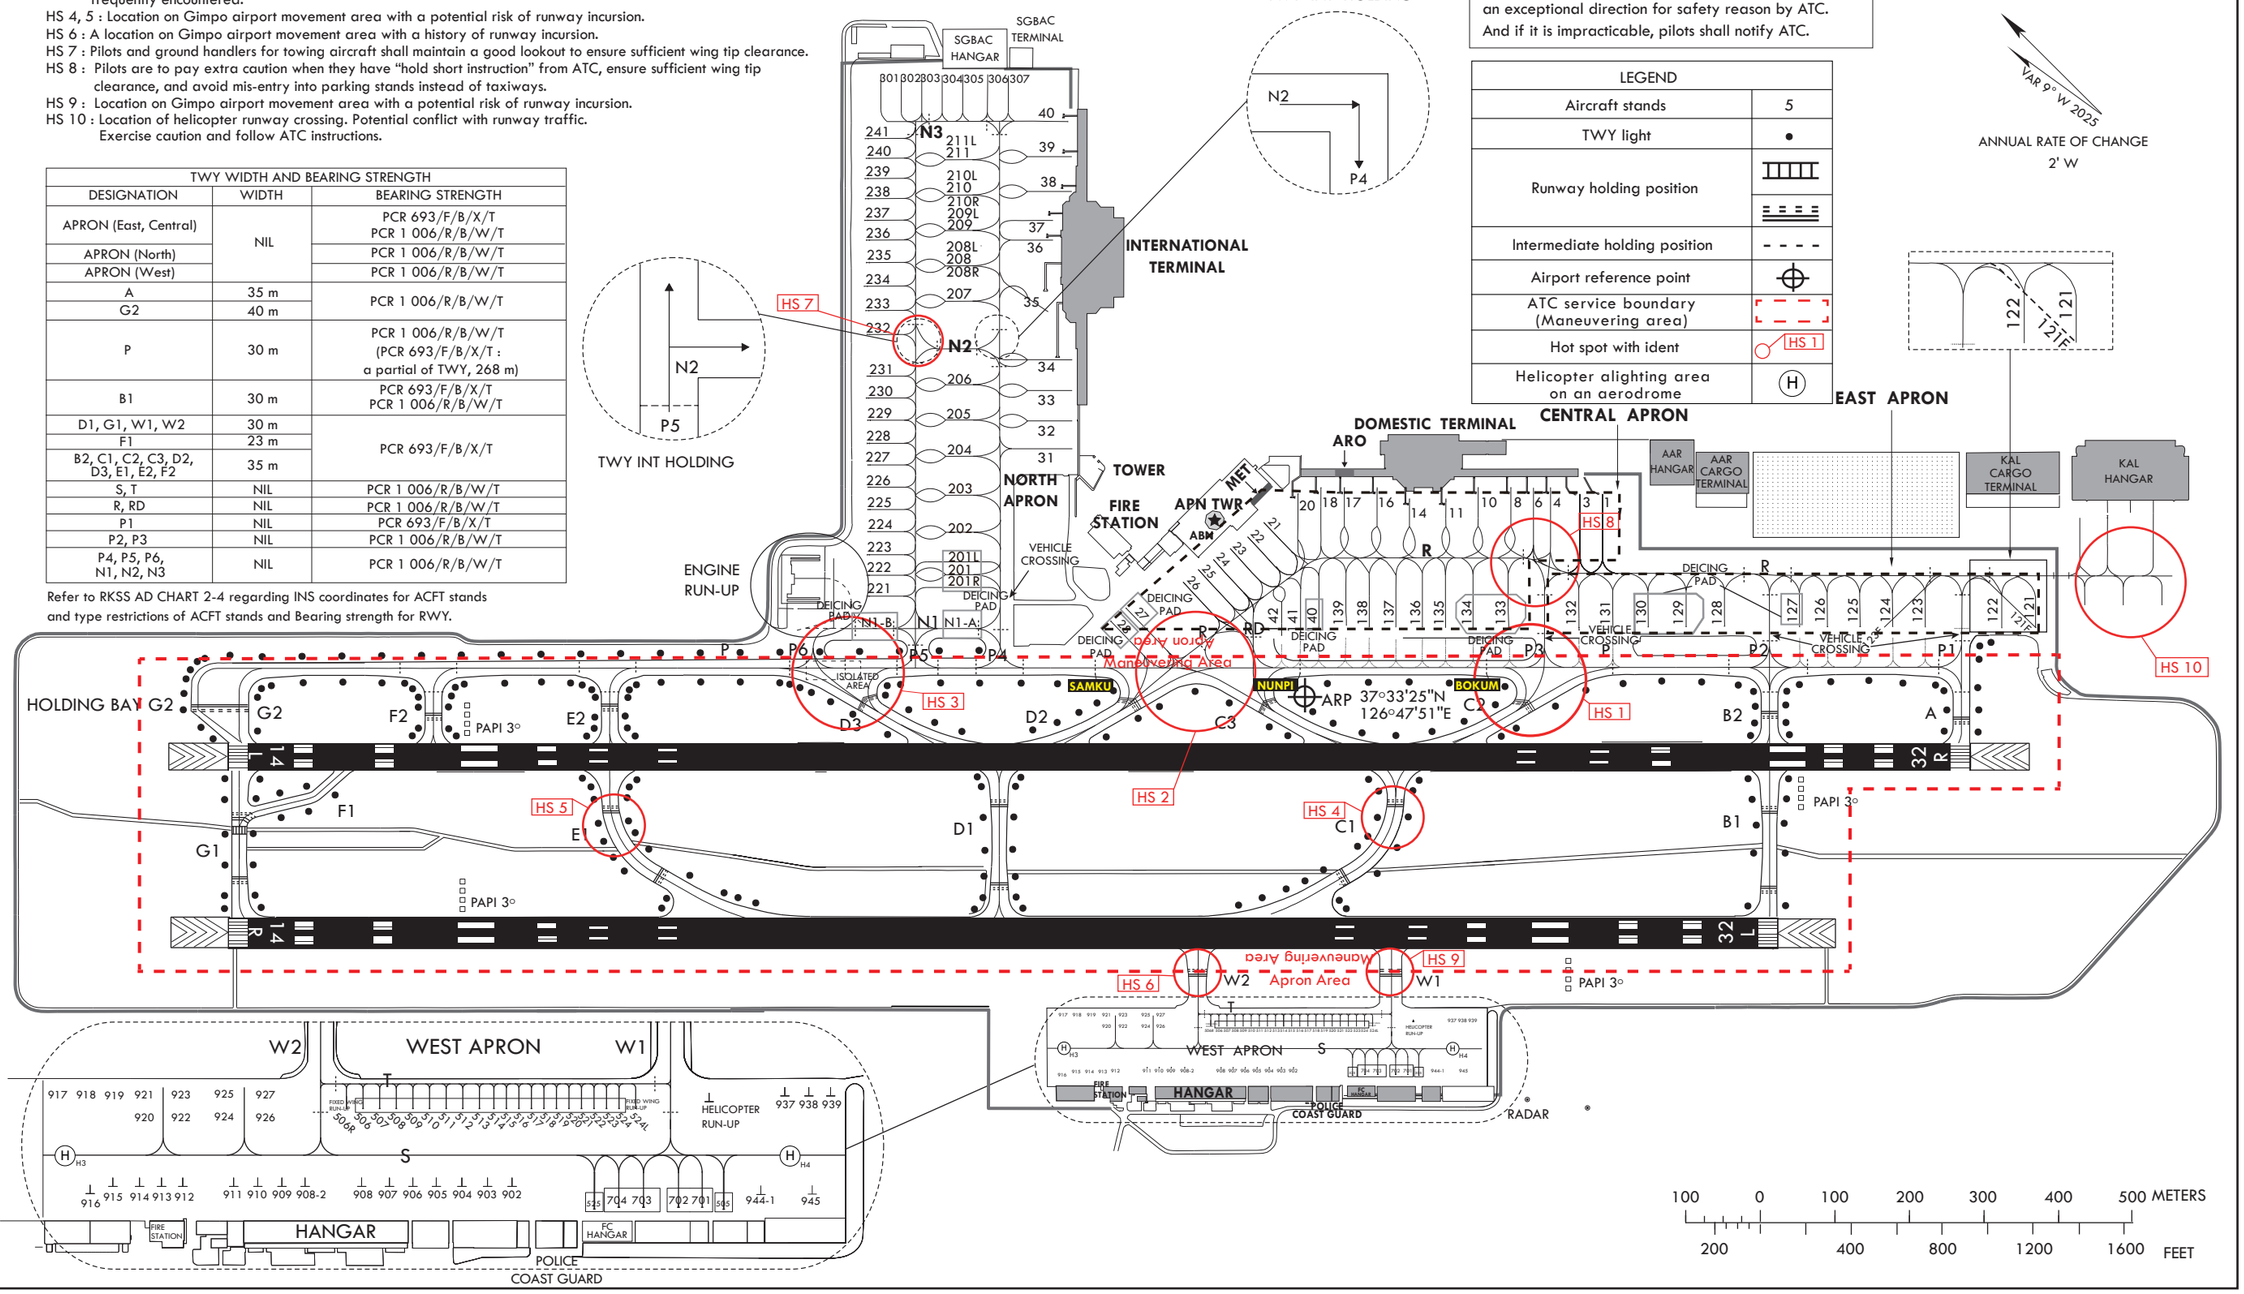

INS COORDINATES FOR AIRCRAFT STANDS (WGS-84)

STAND NR	COORDINATES	STAND NR	COORDINATES	STAND NR	COORDINATES
1	37°33'21.66"N 126°48'19.06"E	202	37°33'50.75"N 126°47'39.70"E	518	37°33'09.95"N 126°47'30.97"E
3	37°33'22.69"N 126°48'17.76"E	203	37°33'52.36"N 126°47'41.86"E	519	37°33'09.63"N 126°47'31.38"E
4	37°33'23.72"N 126°48'16.46"E	204	37°33'54.02"N 126°47'43.95"E	520	37°33'09.31"N 126°47'31.78"E
6	37°33'24.75"N 126°48'15.17"E	205	37°33'55.68"N 126°47'46.38"E	521	37°33'08.99"N 126°47'32.18"E
8	37°33'26.37"N 126°48'13.90"E	206	37°33'57.40"N 126°47'48.06"E	522	37°33'08.67"N 126°47'32.59"E
10	37°33'28.03"N 126°48'11.82"E	207	37°34'01.33"N 126°47'53.11"E	523	37°33'08.35"N 126°47'32.99"E
11	37°33'28.80"N 126°48'09.44"E	208R	37°34'03.12"N 126°47'54.51"E	524	37°33'08.03"N 126°47'33.40"E
14	37°33'30.53"N 126°48'07.28"E	208	37°34'02.99"N 126°47'55.90"E	525	37°33'06.76"N 126°47'28.83"E
16	37°33'32.62"N 126°48'06.03"E	208L	37°34'04.11"N 126°47'55.76"E	701	37°33'04.09"N 126°47'32.21"E
17	37°33'34.16"N 126°48'03.89"E	209	37°34'04.66"N 126°47'57.18"E	702	37°33'04.79"N 126°47'31.35"E
18	37°33'35.37"N 126°48'02.21"E	209L	37°34'05.11"N 126°47'57.02"E	703	37°33'05.63"N 126°47'30.20"E
20	37°33'36.05"N 126°48'00.62"E	210R	37°34'06.45"N 126°47'58.69"E	704	37°33'06.15"N 126°47'29.56"E
21	37°33'36.23"N 126°47'57.36"E	210	37°34'06.32"N 126°47'59.27"E	902	37°33'08.81"N 126°47'27.24"E
22	37°33'36.31"N 126°47'55.39"E	210L	37°34'07.44"N 126°47'59.95"E	903	37°33'09.51"N 126°47'26.33"E
23	37°33'36.33"N 126°47'53.74"E	211	37°34'07.98"N 126°48'01.36"E	904	37°33'10.17"N 126°47'25.52"E
24	37°33'36.41"N 126°47'52.04"E	211L	37°34'08.44"N 126°48'01.20"E	905	37°33'10.82"N 126°47'24.70"E
25	37°33'36.98"N 126°47'50.47"E	221	37°33'52.40"N 126°47'30.17"E	906	37°33'11.48"N 126°47'23.89"E
26	37°33'37.59"N 126°47'48.82"E	222	37°33'53.40"N 126°47'31.43"E	907	37°33'12.14"N 126°47'23.07"E
27	37°33'39.32"N 126°47'44.18"E	223	37°33'54.40"N 126°47'32.68"E	908	37°33'12.80"N 126°47'22.26"E
28	37°33'39.15"N 126°47'42.44"E	224	37°33'55.34"N 126°47'34.10"E	908-2	37°33'14.20"N 126°47'20.50"E
31	37°33'49.67"N 126°47'49.77"E	225	37°33'56.34"N 126°47'35.26"E	909	37°33'14.88"N 126°47'19.66"E
32	37°33'51.06"N 126°47'51.47"E	226	37°33'57.34"N 126°47'36.51"E	910	37°33'15.53"N 126°47'18.85"E
33	37°33'52.81"N 126°47'53.66"E	227	37°33'58.34"N 126°47'37.76"E	911	37°33'16.17"N 126°47'18.04"E
34	37°33'54.55"N 126°47'55.84"E	228	37°33'59.33"N 126°47'39.14"E	912	37°33'17.41"N 126°47'16.36"E
35	37°33'57.13"N 126°47'57.81"E	229	37°34'00.33"N 126°47'40.27"E	913	37°33'18.00"N 126°47'15.62"E
36	37°33'59.85"N 126°48'01.16"E	230	37°34'01.33"N 126°47'41.52"E	914	37°33'18.59"N 126°47'14.88"E
37	37°34'00.78"N 126°48'02.33"E	231	37°34'02.33"N 126°47'42.77"E	915	37°33'19.20"N 126°47'14.12"E
38	37°34'01.91"N 126°48'05.38"E	232	37°34'04.42"N 126°47'45.40"E	916	37°33'19.62"N 126°47'13.19"E
39	37°34'03.45"N 126°48'07.50"E	233	37°34'05.42"N 126°47'46.66"E	917	37°33'22.94"N 126°47'15.24"E
40	37°34'05.14"N 126°48'09.63"E	234	37°34'06.46"N 126°47'47.84"E	918	37°33'22.21"N 126°47'16.17"E
121	37°32'55.01"N 126°48'37.35"E	235	37°34'07.46"N 126°47'49.97"E	919	37°33'21.48"N 126°47'17.09"E
121F	37°32'54.94"N 126°48'37.21"E	236	37°34'08.46"N 126°47'50.35"E	920	37°33'20.29"N 126°47'17.07"E
122	37°32'56.61"N 126°48'35.34"E	237	37°34'09.46"N 126°47'51.60"E	921	37°33'20.88"N 126°47'17.82"E
123	37°33'00.19"N 126°48'30.72"E	238	37°34'10.45"N 126°47'52.85"E	922	37°33'19.02"N 126°47'18.68"E
123F	37°33'01.94"N 126°48'28.35"E	239	37°34'11.45"N 126°47'54.11"E	923	37°33'19.61"N 126°47'19.41"E
124	37°33'01.72"N 126°48'28.74"E	240	37°34'12.45"N 126°47'55.36"E	924	37°33'18.14"N 126°47'19.81"E
125	37°33'03.25"N 126°48'26.78"E	241	37°34'13.45"N 126°47'56.61"E	925	37°33'18.72"N 126°47'20.53"E
126	37°33'04.80"N 126°48'24.83"E	301	37°34'16.12"N 126°48'01.33"E	926	37°33'16.88"N 126°47'21.38"E
127	37°33'06.03"N 126°48'23.26"E	302	37°34'15.22"N 126°48'02.47"E	927	37°33'17.46"N 126°47'22.11"E
128	37°33'09.73"N 126°48'18.72"E	303	37°34'14.35"N 126°48'03.63"E	937	37°33'03.92"N 126°47'39.23"E
129	37°33'11.55"N 126°48'16.44"E	304	37°34'13.71"N 126°48'05.17"E	938	37°33'03.37"N 126°47'39.92"E
130	37°33'13.42"N 126°48'14.14"E	305	37°34'12.14"N 126°48'06.34"E	939	37°33'02.82"N 126°47'40.62"E
131	37°33'14.99"N 126°48'12.01"E	306	37°34'11.15"N 126°48'07.76"E	944-1	37°33'01.85"N 126°47'35.40"E
132	37°33'16.61"N 126°48'10.05"E	307	37°34'10.69"N 126°48'08.92"E	945	37°33'00.76"N 126°47'36.74"E
133	37°33'19.96"N 126°48'05.76"E	505	37°33'03.28"N 126°47'33.12"E		
134	37°33'21.63"N 126°48'03.67"E	506	37°33'14.76"N 126°47'24.92"E		
135	37°33'22.97"N 126°48'02.00"E	507	37°33'14.32"N 126°47'25.46"E		
136	37°33'24.37"N 126°48'00.31"E	508	37°33'13.88"N 126°47'26.01"E		
137	37°33'25.52"N 126°47'58.89"E	509	37°33'13.45"N 126°47'26.56"E		
138	37°33'26.65"N 126°47'57.44"E	510	37°33'13.01"N 126°47'27.11"E		
139	37°33'27.66"N 126°47'56.39"E	511	37°33'12.57"N 126°47'27.66"E		
140	37°33'28.81"N 126°47'54.72"E	512	37°33'12.14"N 126°47'28.20"E		
141	37°33'29.57"N 126°47'53.35"E	513	37°33'11.72"N 126°47'28.75"E		
142	37°33'30.47"N 126°47'52.15"E	514	37°33'11.29"N 126°47'29.28"E		
201	37°33'48.61"N 126°47'37.13"E	515	37°33'10.91"N 126°47'29.76"E		
201R	37°33'48.36"N 126°47'36.13"E	516	37°33'10.59"N 126°47'30.16"E		
201L	37°33'49.37"N 126°47'37.40"E	517	37°33'10.27"N 126°47'30.57"E		

RWY	DIRECTION (MAGNETIC)	THR (WGS-84)	BEARING STRENGTH
14R	144°	37°34'06"N 126°46'32"E	PCR 693/F/B/X/T Asphalt
32L	324°	37°32'53"N 126°48'04"E	
14L	144°	37°34'15"N 126°46'42"E	- PCR 693/F/B/X/T Asphalt - PCR 1 006/R/B/W/T Concrete (156 m from RWY THR)
32R	324°	37°32'52"N 126°48'26"E	- PCR 693/F/B/X/T Asphalt - PCR 1 006/R/B/W/T Concrete (151 m from RWY THR)
APRONS		East & Central	PCR 693/F/B/X/T PCR 1 006/R/B/W/T
		North	PCR 1 006/R/B/W/T
		West	PCR 1 006/R/B/W/T

STANDS NUMBER	AIRCRAFT TYPE
121F, 123F	A380-800, B747-8
10, 16, 32, 33, 34, 38, 40, 133, 134, 201, 202, 203, 204, 205, 207, 208, 209, 210, 211	B747-400, A340-600
35, 128, 129, 131	B747-400, A350-900
39	B777-300, A330-300
8, 17, 121, 124, 125, 132	B777-200, A330-300
126, 130, 137, 206	B767-300
1, 3, 4, 6, 11, 14, 18, 20, 21, 22, 23, 24, 25, 26, 27, 28, 31, 36, 37, 122, 123, 127, 135, 136, 138, 139, 140, 141, 142, 201R, 201L, 208R, 208L, 209L, 210R, 210L, 211L, 222, 223, 224, 225, 226, 227, 228, 229, 230, 231, 232, 233, 234, 235, 236, 237, 238, 239, 240, 241, 301, 302, 303, 304, 305, 306, 307	B737MAX9, A321NEO
221	B737-900, A321-200

* Code letter “D” and above aircraft are prohibited from taxiing out of all aircraft stands and performing forward towing operations.
* Aircraft stands NR 123-127, 131-142, 201-211 may be used by aircraft of ICAO code letter “C” or lower for self-maneuvering, subject to prior permission from ATC.
* Taxiway intersection markings are provided for 5 places in front of the intersections / junctions on apron taxiway P4 and P5.
* Isolated area : At the intersection of TWY D3 and TWY P.
* De-icing pad

  B737 MAX 9, A321 NEO : 27, 28, 140, 127 and 201L/R
  B747-400, A350-900 : 129
  B767-300 : 130
  B747-400, A340-600 : 133, 134, N-1A, N-1B, 201
* Engine Run-up : Front of "P6" TWY
* Multiple Aircraft Ramp System(MARS) : 121F(121, 122), 123F(123, 124), 201L(201), 201R(201), 208L(208), 208R(208), 209L(209), 210L(210), 210R(210), 211L(211)

Aircraft Classification	Stand		Remarks
	Number	Dimensions(m)	
Helicopter	908-2, 902, 945	19×19	BELL214B-1
	903~908, 909~911	17.8×17.8	MI-2
	912~927, 944-1	16×16	KA32-T
	937~939	15×15	EC-155B1
Fixed-wing	701, 702	25.8×21.4	CN235
	703, 704	20.86×19.61	CL-605
	515~524	9×11	C172R
	505~514, 525	13×16	C-208B

* Dimensions means overall length × width
* Any Fixed-wing aircraft of wingspan exceed 16 m is prohibited to use Fixed-wing run up pad(524L/506R).

Change : Amended THR coordinates of RWY 14R/L.