AERODROME GROUND MOVEMENT CHART - ICAO

APRON ELEV
ELEV **105** ft

TWR	126.2	236.6	365.0
GND	121.95	275.8	

DAEGU/Daegu INTL

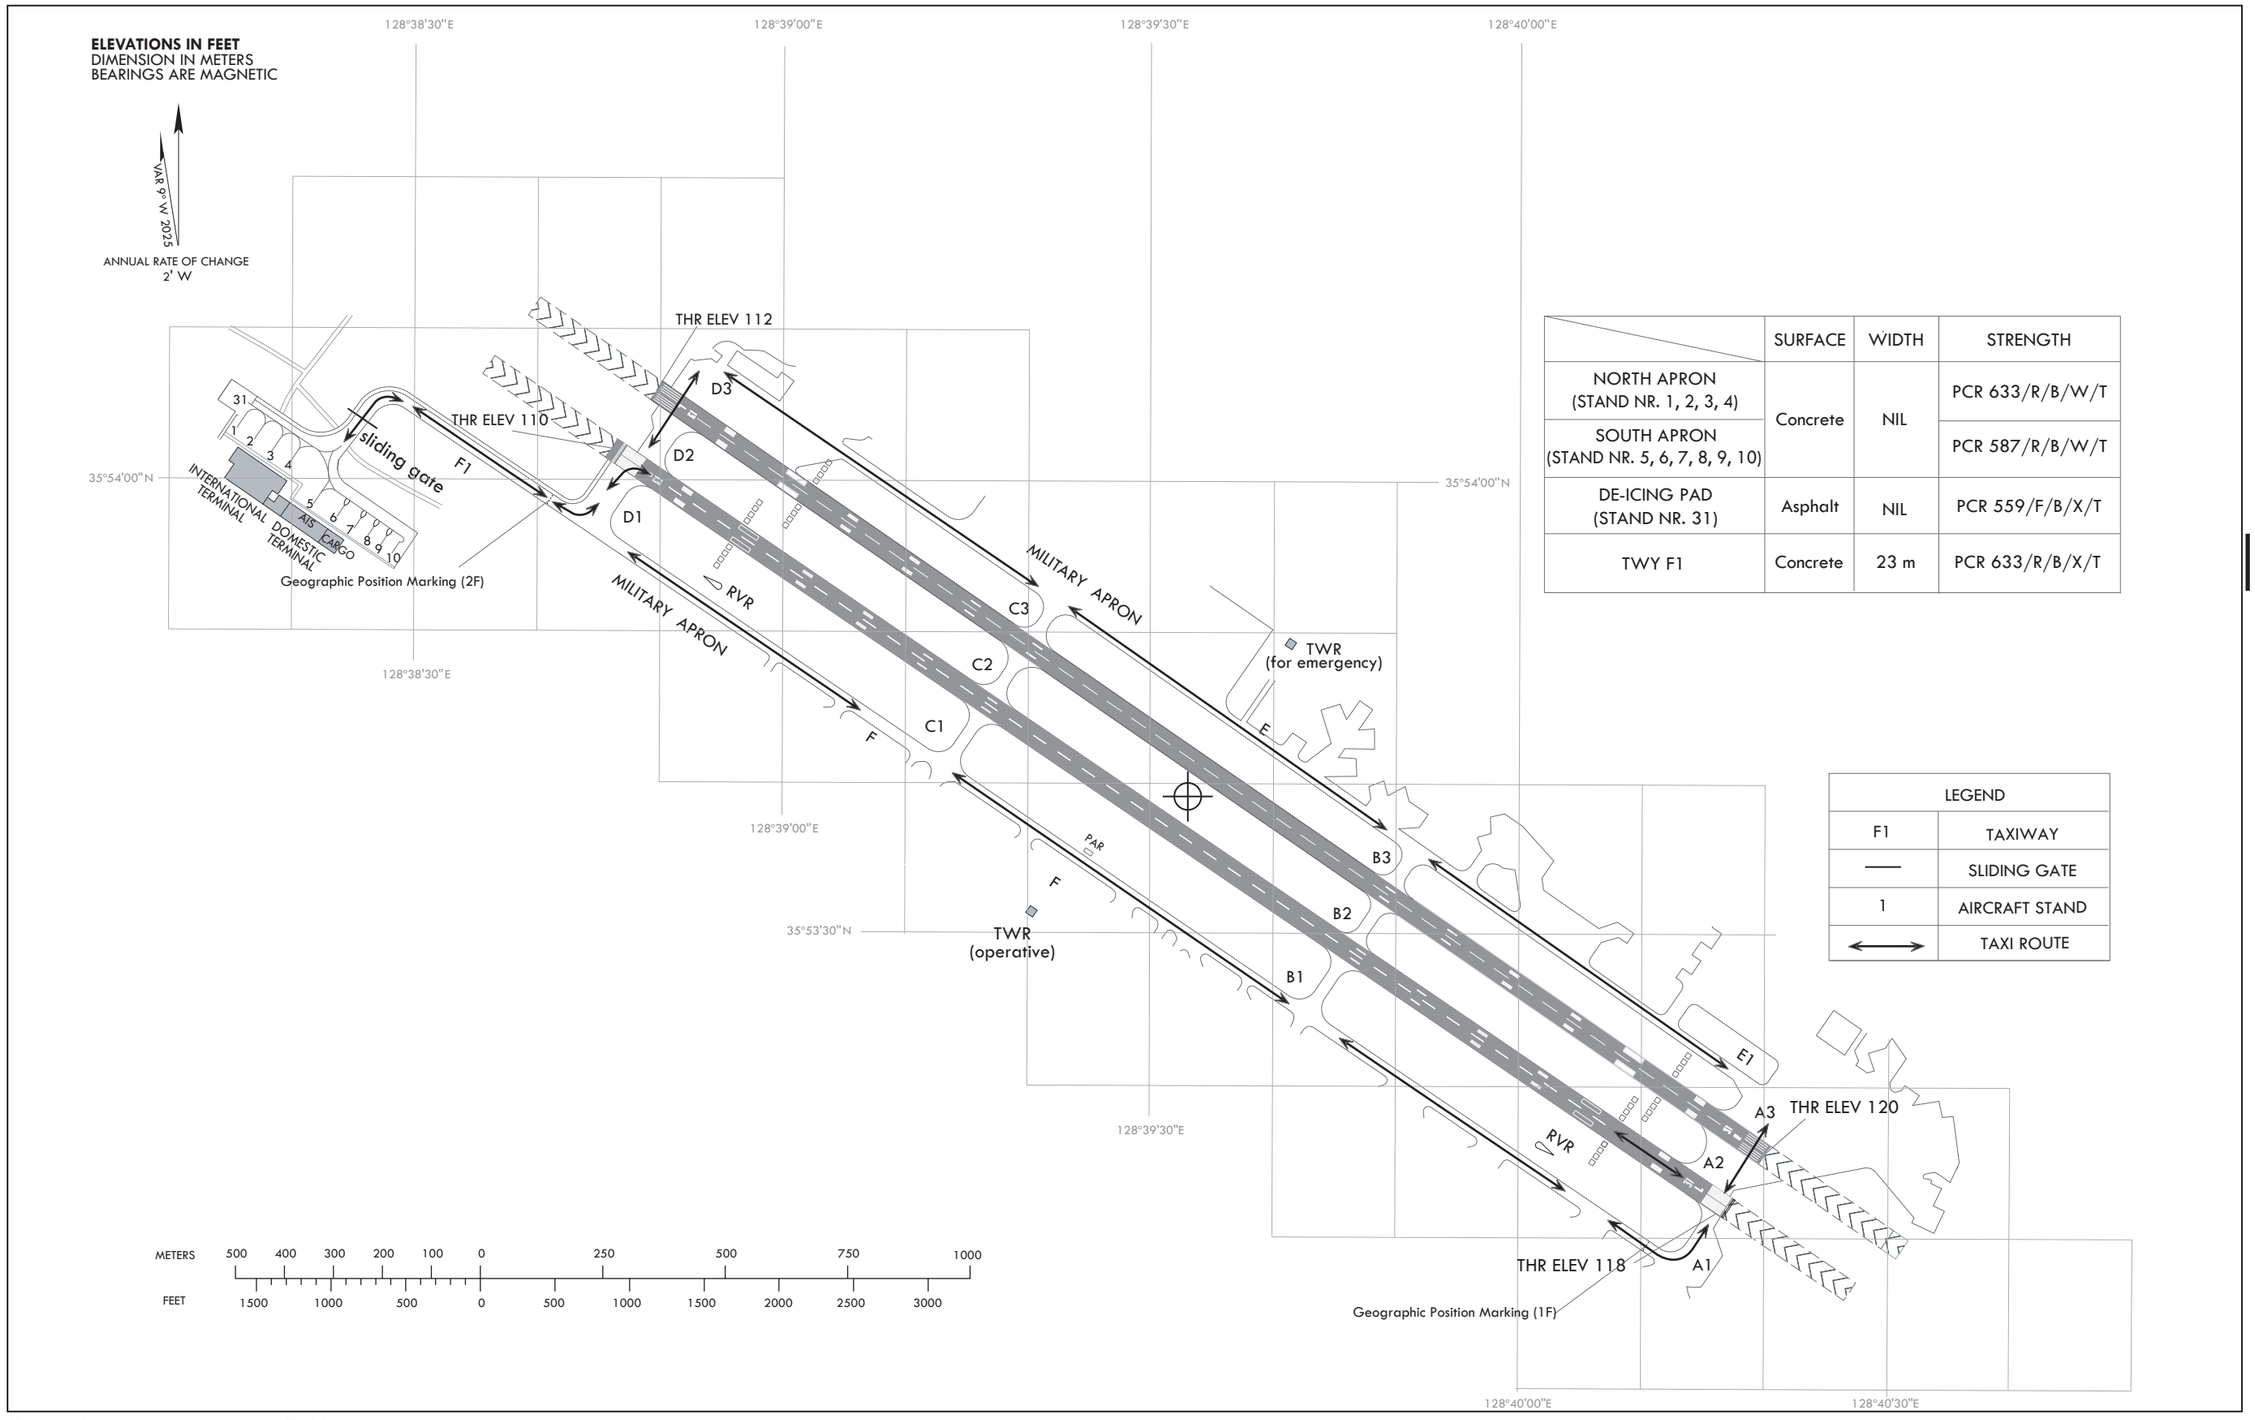

	SURFACE	WIDTH	STRENGTH
NORTH APRON (STAND NR. 1, 2, 3, 4)	Concrete	NIL	PCR 633/R/B/W/T
SOUTH APRON (STAND NR. 5, 6, 7, 8, 9, 10)			PCR 587/R/B/W/T
DE-ICING PAD (STAND NR. 31)	Asphalt	NIL	PCR 559/F/B/X/T
TWY F1	Concrete	23 m	PCR 633/R/B/X/T

LEGEND	
F1	TAXIWAY
——	SLIDING GATE
1	AIRCRAFT STAND
⟷	TAXI ROUTE

Change : Information of surface for TWY.